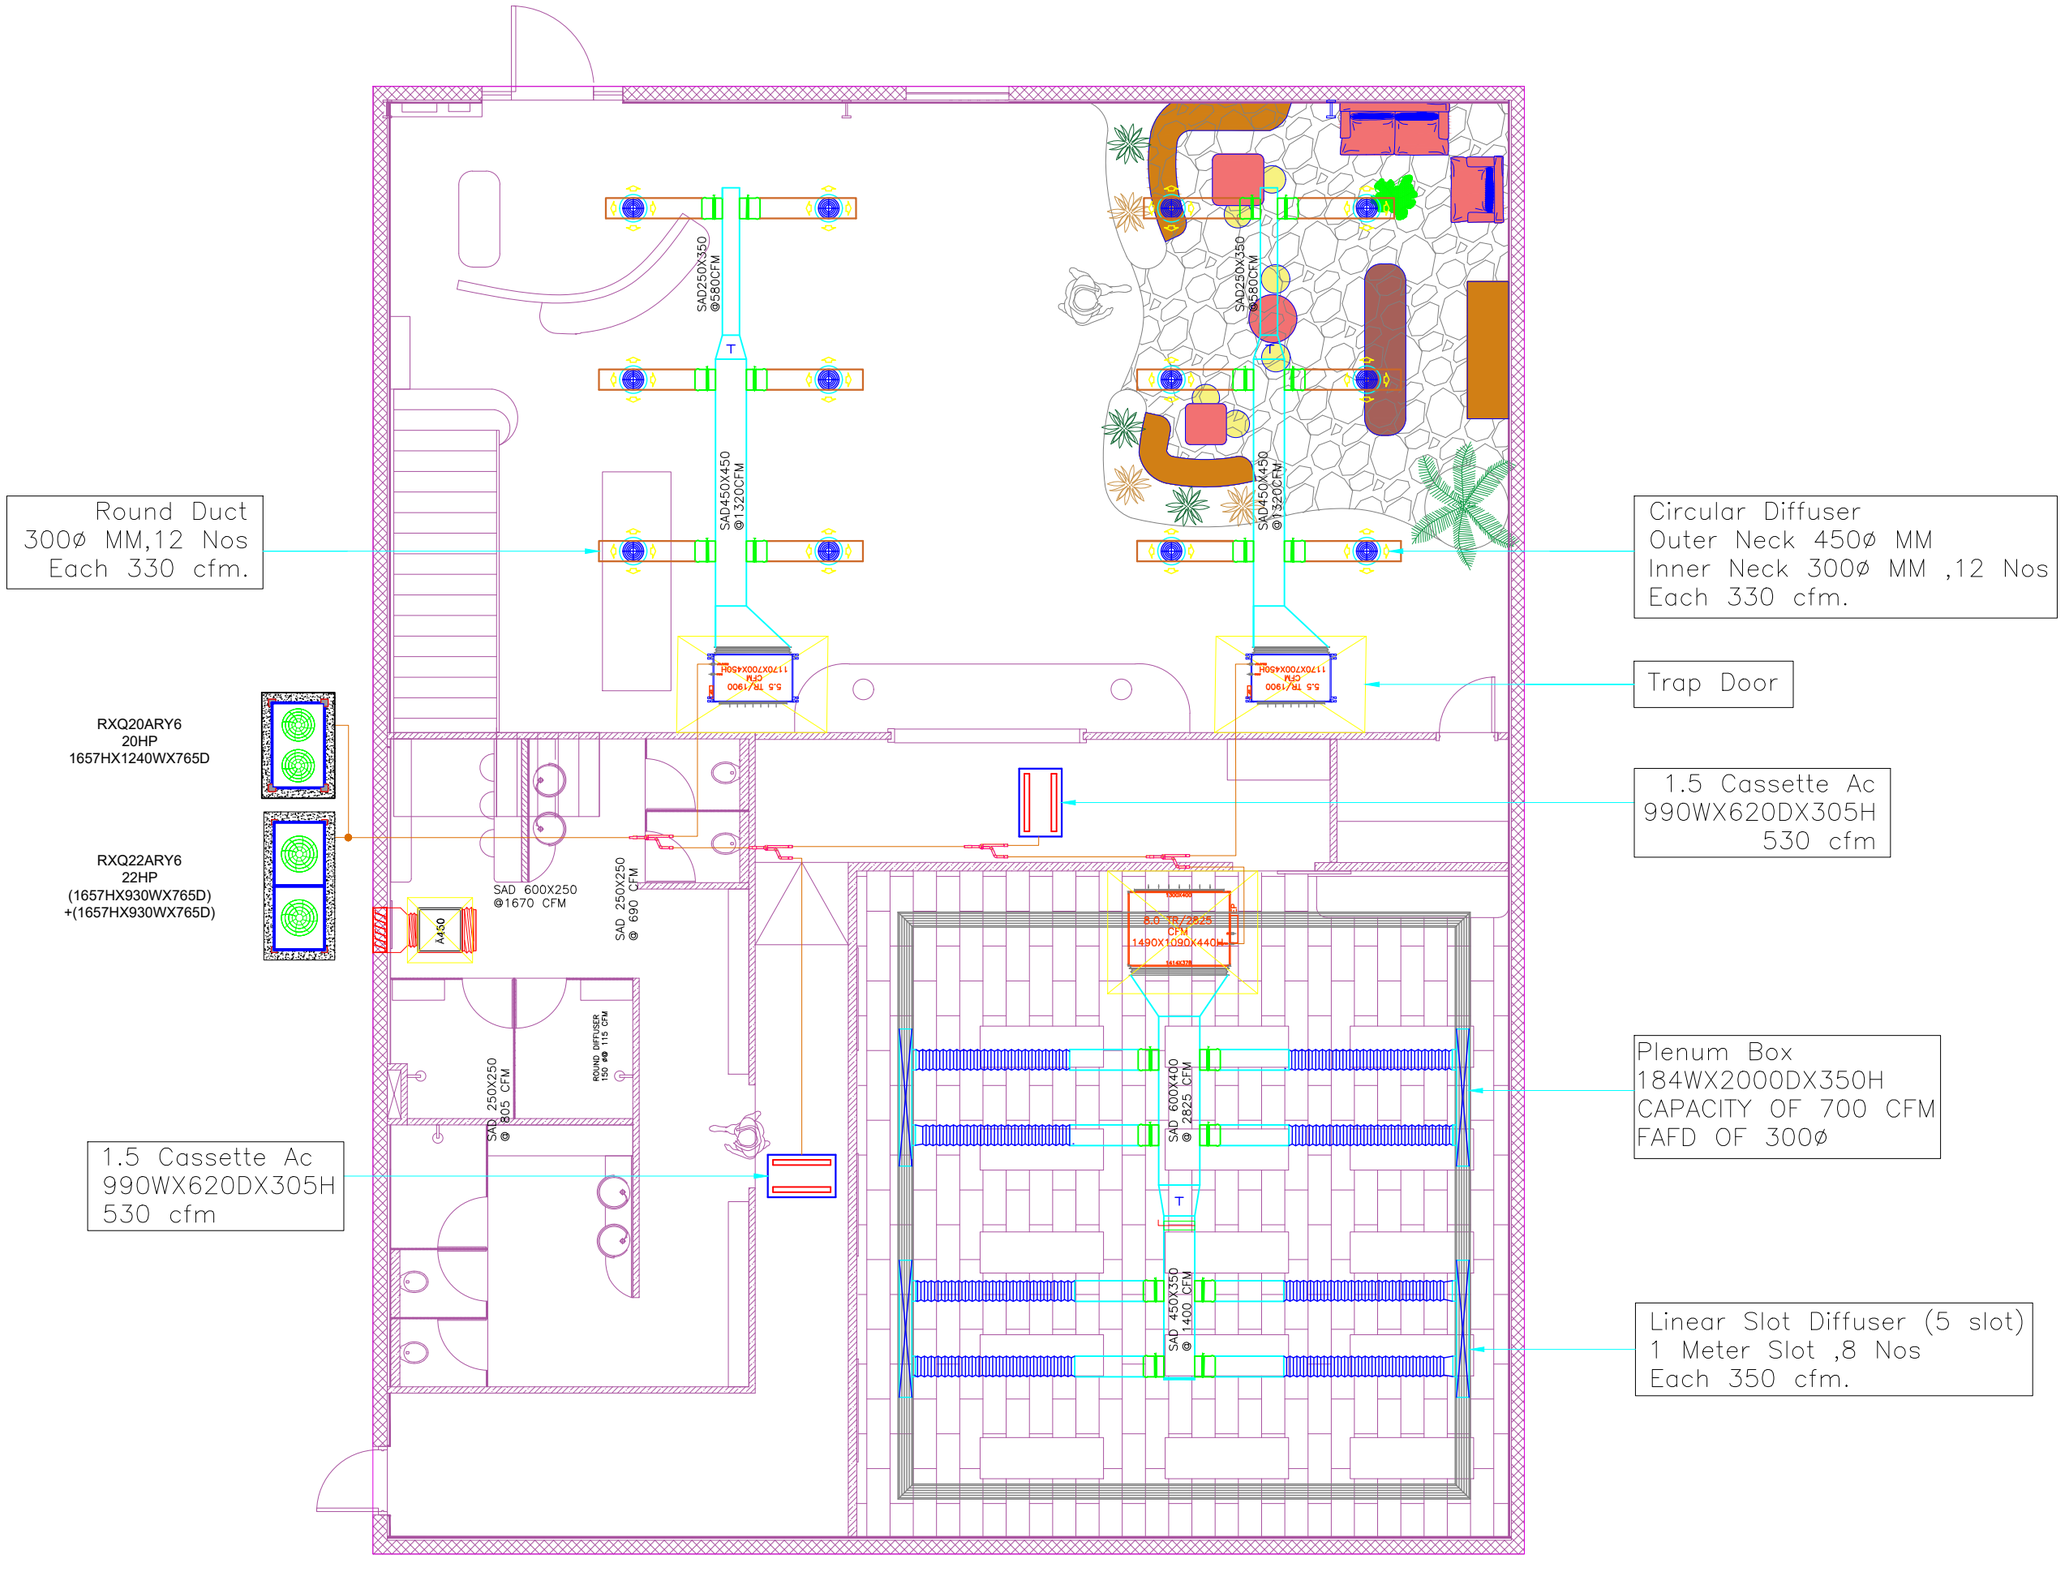


GF AC

SITE PLAN :

NOTE :

PROJECT :

YOGA CENTRE

SR NO	DATE	DESCRIPTIONS	DRWN BY
		ISSUED FOR APPROVAL	


CLIENT :

MAIN CONTRACTOR :

MEP CONSULTANT:

BenderZ Design & Consultant

PROJECT NO:	IND-001	
DRAWING TITLE:	GROUND FLOOR - HVAC DUCT DRAWING	
DRAWING NO :		DATE:
DRAWN BY:	CHECKED BY:	SCALE:
SERIAL NO:	SHEET NO:	REV.NO:

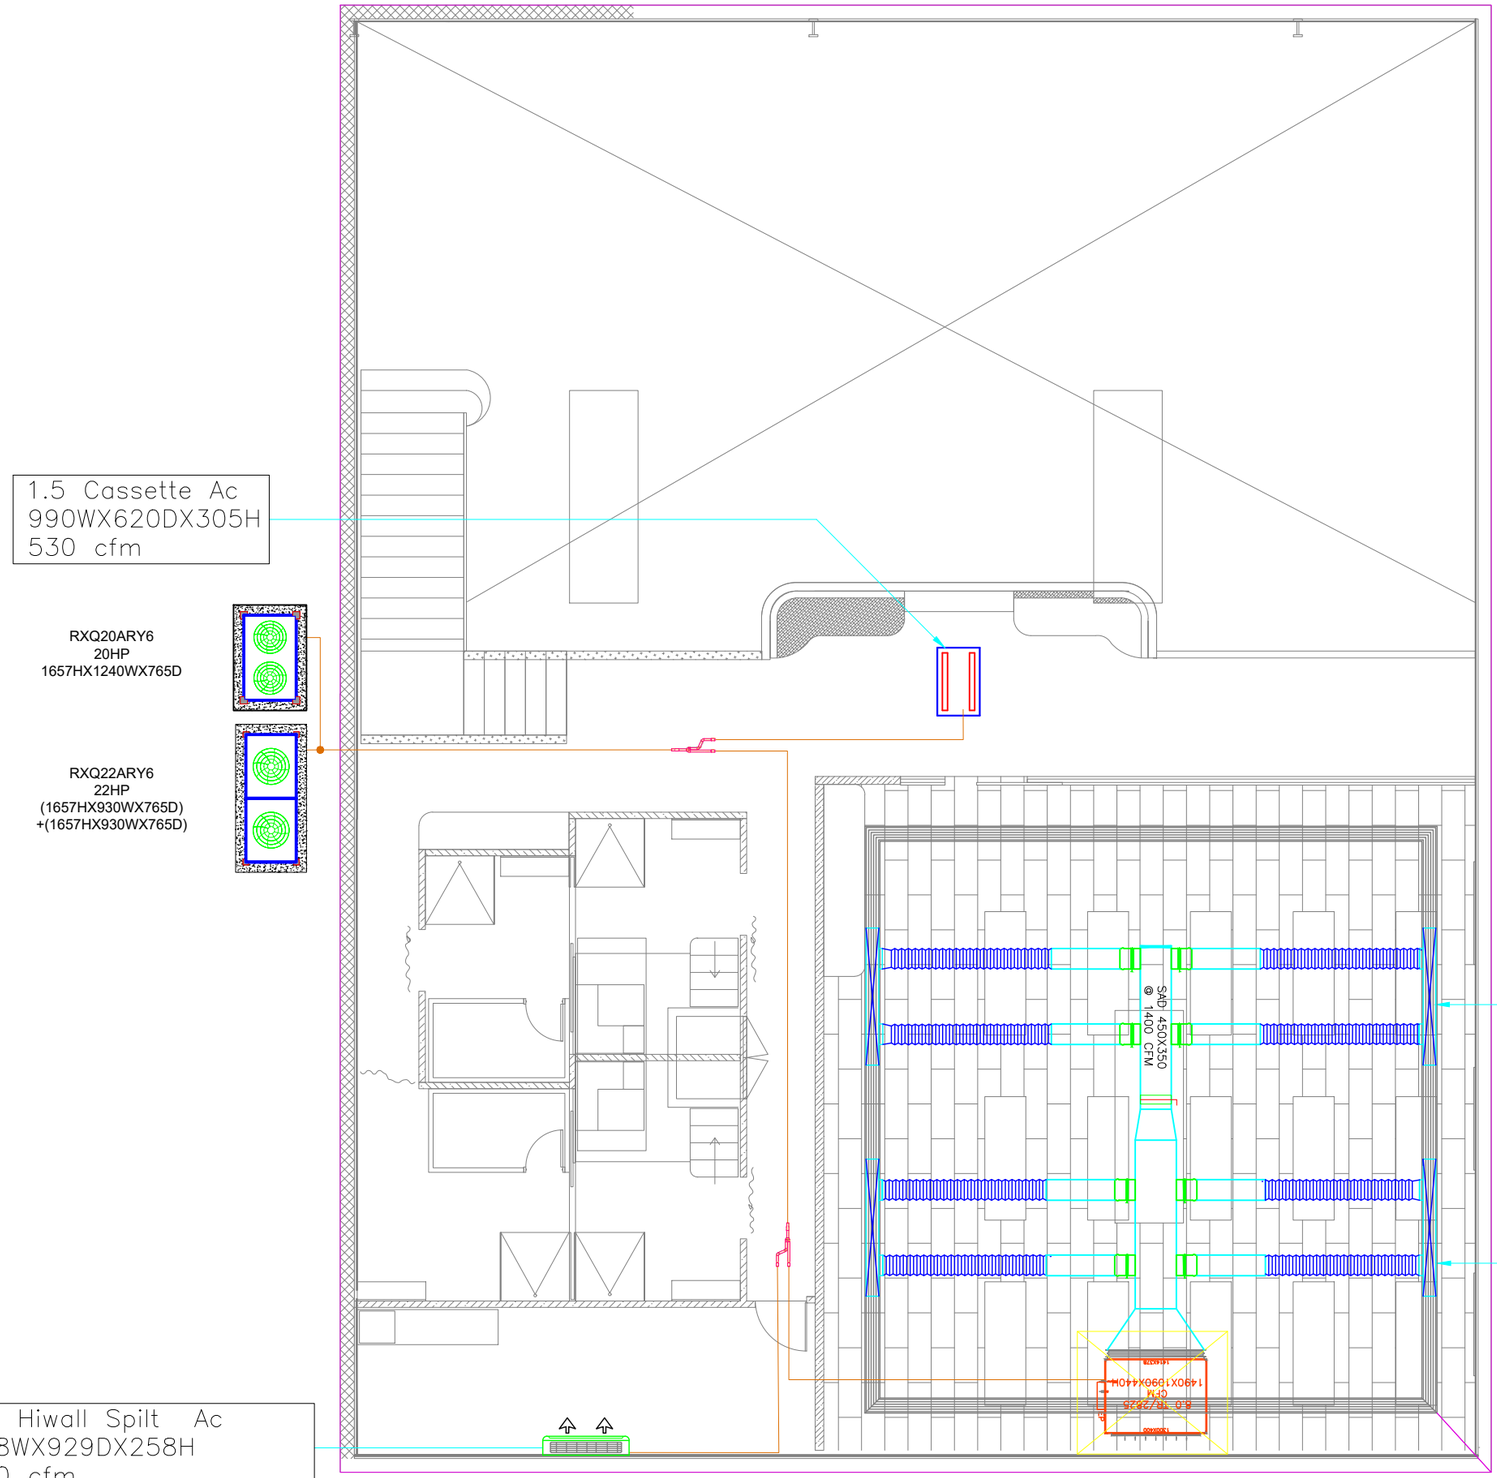

MF AC

SITE PLAN :

NOTE :

PROJECT :

YOGA CENTRE

SR NO	DATE	DESCRIPTIONS	DRWN BY
		ISSUED FOR APPROVAL	


CLIENT :

MAIN CONTRACTOR :

MEP CONSULTANT:

BenderZ Design & Consultant

PROJECT NO:		
DRAWING TITLE: MEZZANINE FLOOR - HVAC DUCT DRAWING		
DRAWING NO :		DATE:
DRAWN BY:	CHECKED BY:	SCALE:
SERIAL NO:	SHEET NO:	REV.NO:

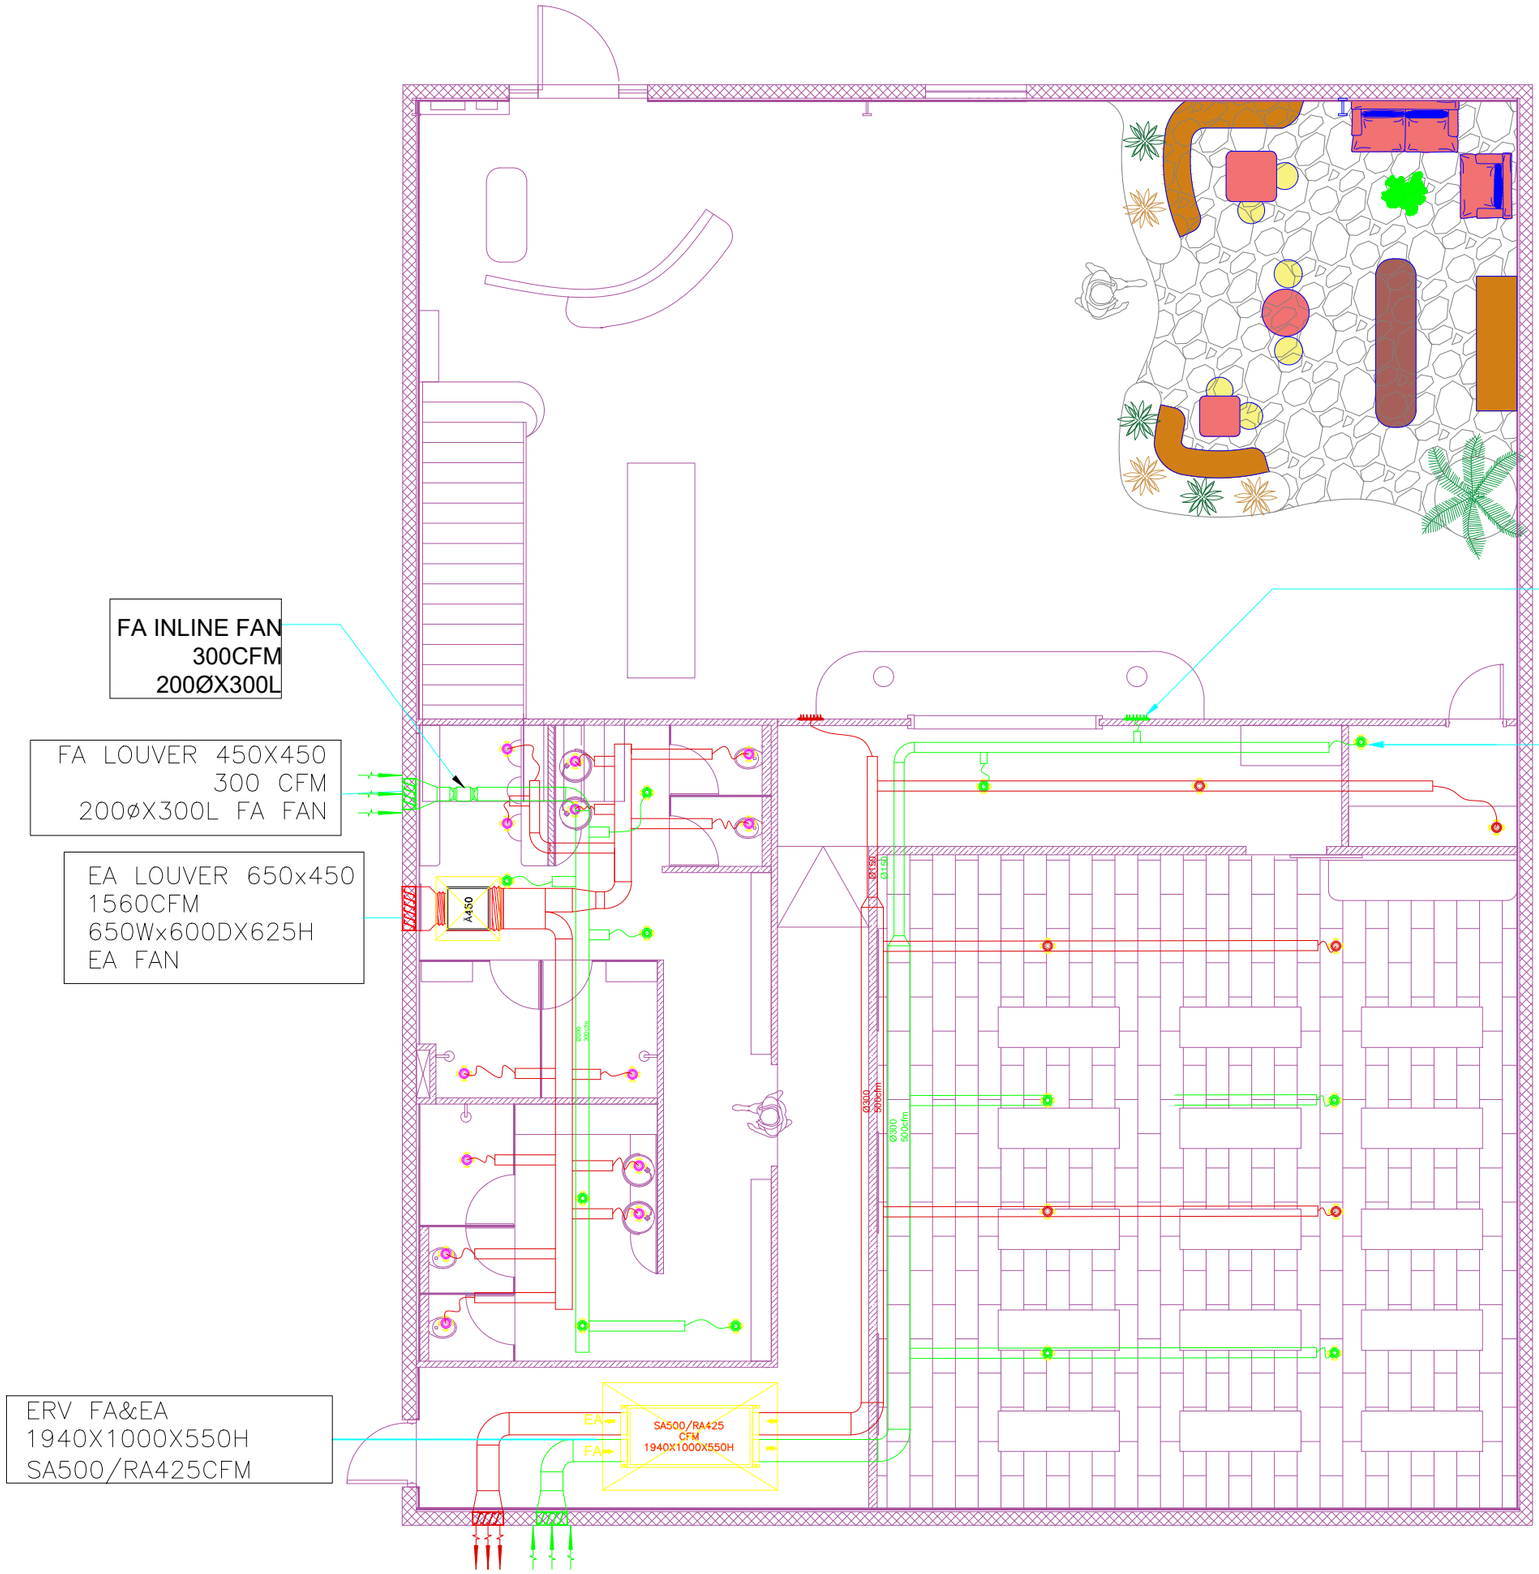

GF FA AND EA

SITE PLAN :

NOTE :

PROJECT :

YOGA CENTRE

SR NO	DATE	DESCRIPTIONS	DRWN BY
		ISSUED FOR APPROVAL	


CLIENT :

MAIN CONTRACTOR :

MEP CONSULTANT:

BenderZ Design & Consultant

PROJECT NO:		
DRAWING TITLE: GROUND FLOOR - HVAC FRESH AIR AND EXHAUST AIR		
DRAWING NO :		DATE:
DRAWN BY:	CHECKED BY:	SCALE:
SERIAL NO:	SHEET NO:	REV.NO:

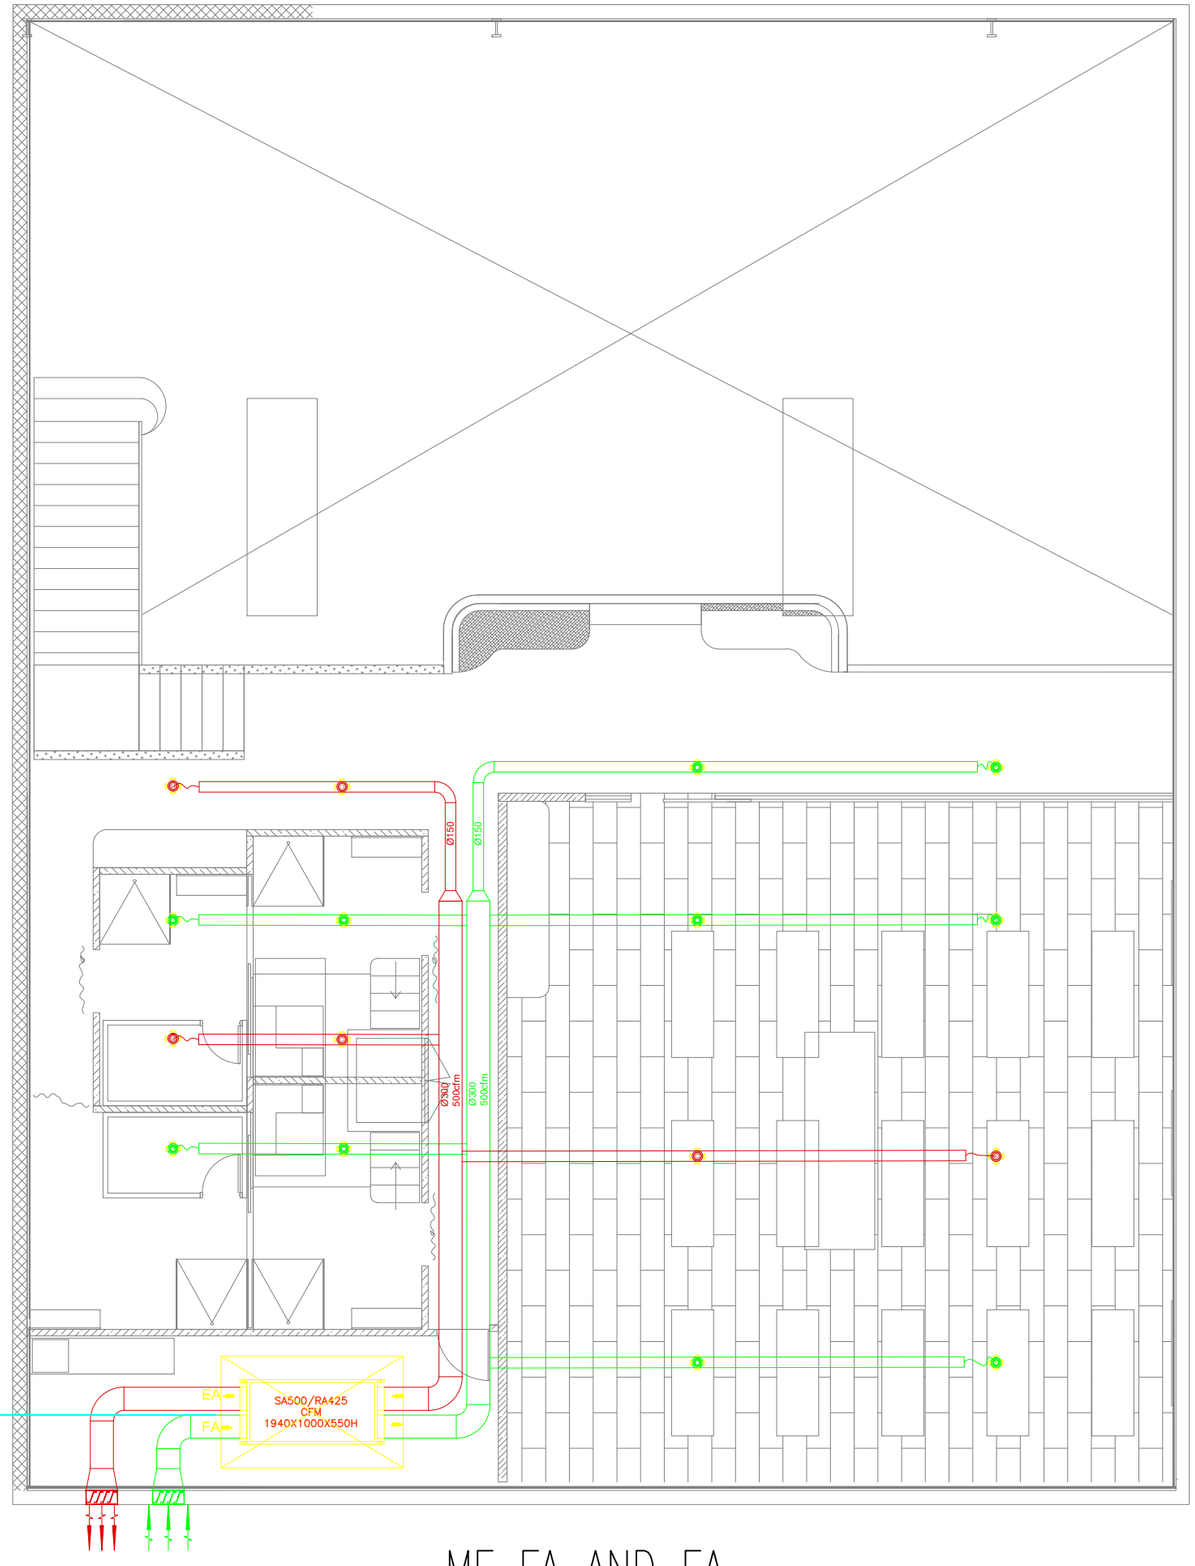

ERV FA&EA
1940X1000X550H
SA500/RA425CFM

FA AND EA
LOUVER 450X450

MF FA AND EA

SITE PLAN :

NOTE :

PROJECT :

YOGA CENTRE

SR NO	DATE	DESCRIPTIONS	DRWN BY
		ISSUED FOR APPROVAL	


CLIENT :

MAIN CONTRACTOR :

MEP CONSULTANT:

BenderZ Design & Consultant

PROJECT NO:		
DRAWING TITLE: MEZZANINE FLOOR - HVAC FRESH AIR AND EXHAUST AIR		
DRAWING NO :		DATE:
DRAWN BY:	CHECKED BY:	SCALE:
SERIAL NO:	SHEET NO:	REV.NO:

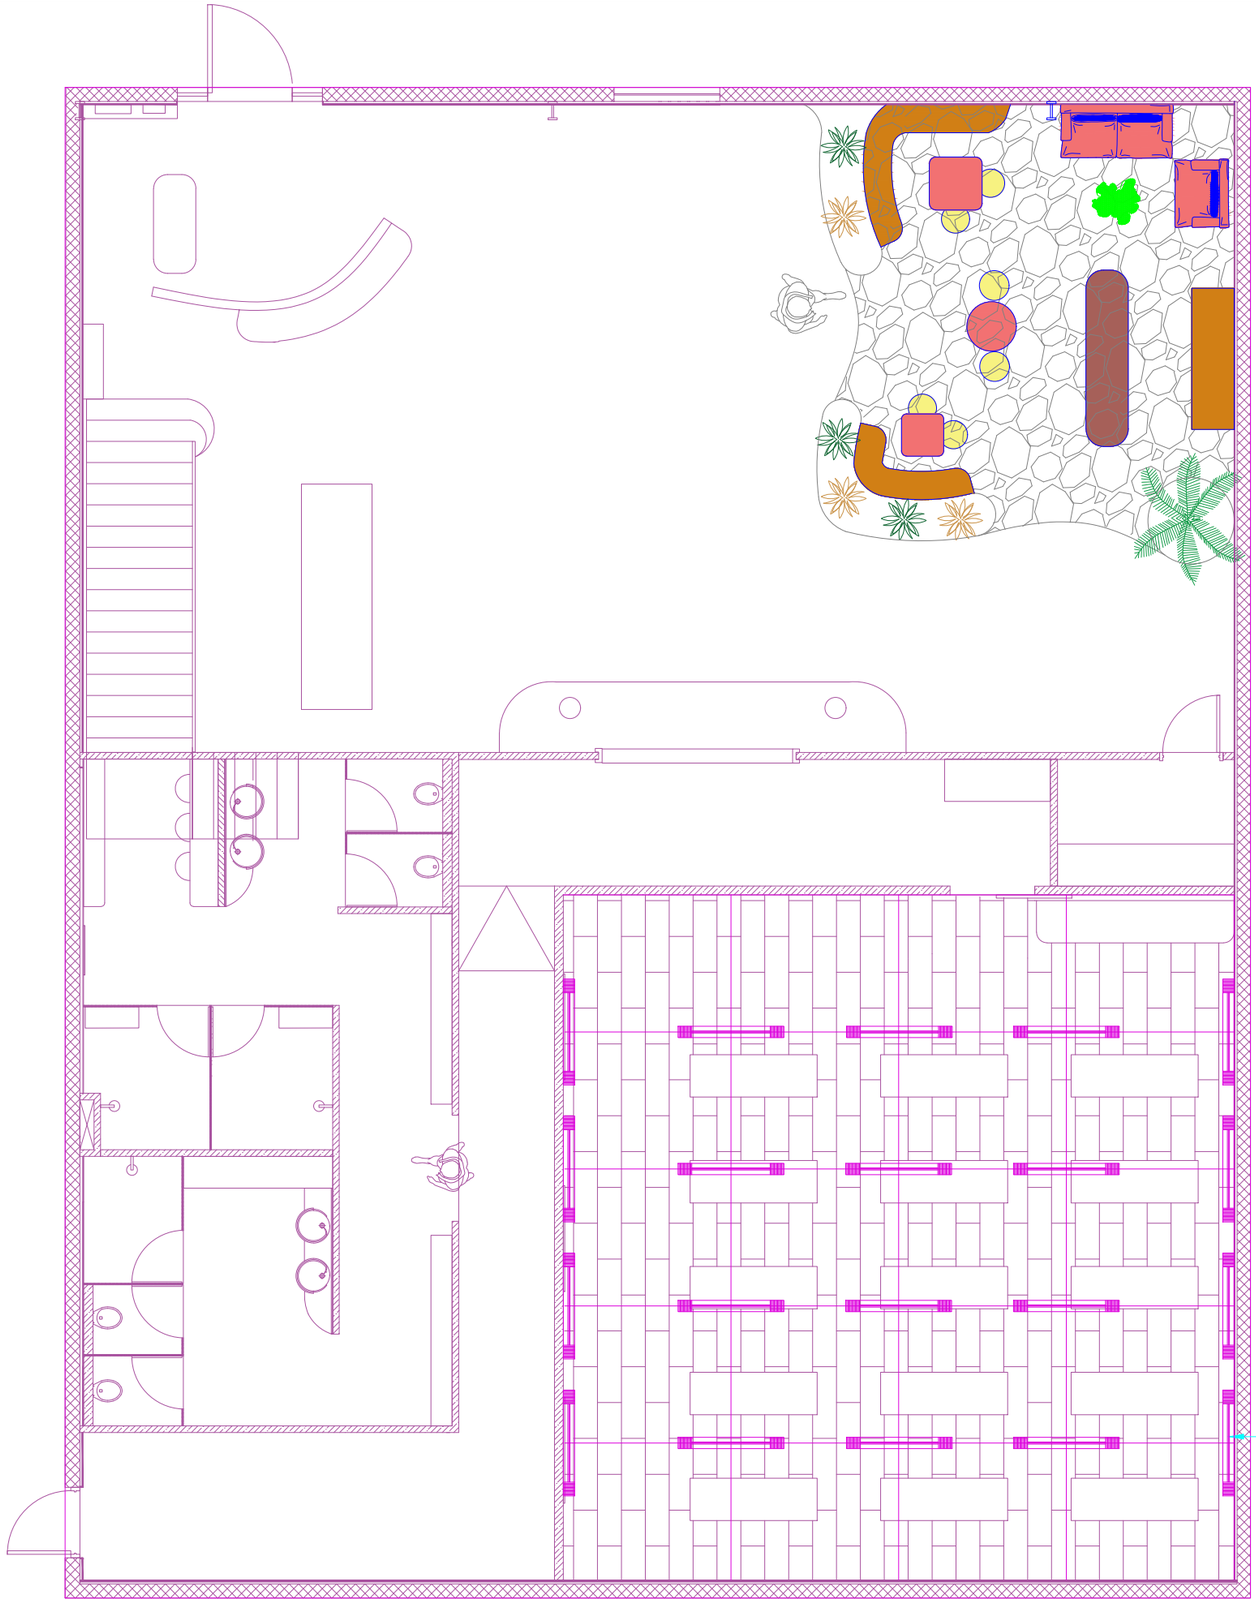

GROUND FLOOR

SITE PLAN :

NOTE :

PROJECT :

YOGA CENTRE

SR NO	DATE	DESCRIPTIONS	DRWN BY
		ISSUED FOR APPROVAL	

CLIENT :

MAIN CONTRACTOR :

MEP CONSULTANT:

BenderZ Design & Consultant

PROJECT NO:		
DRAWING TITLE: GROUND FLOOR - HVAC HEATING STRIP		
DRAWING NO :		DATE:
DRAWN BY:	CHECKED BY:	SCALE:
SERIAL NO:	SHEET NO:	REV.NO: