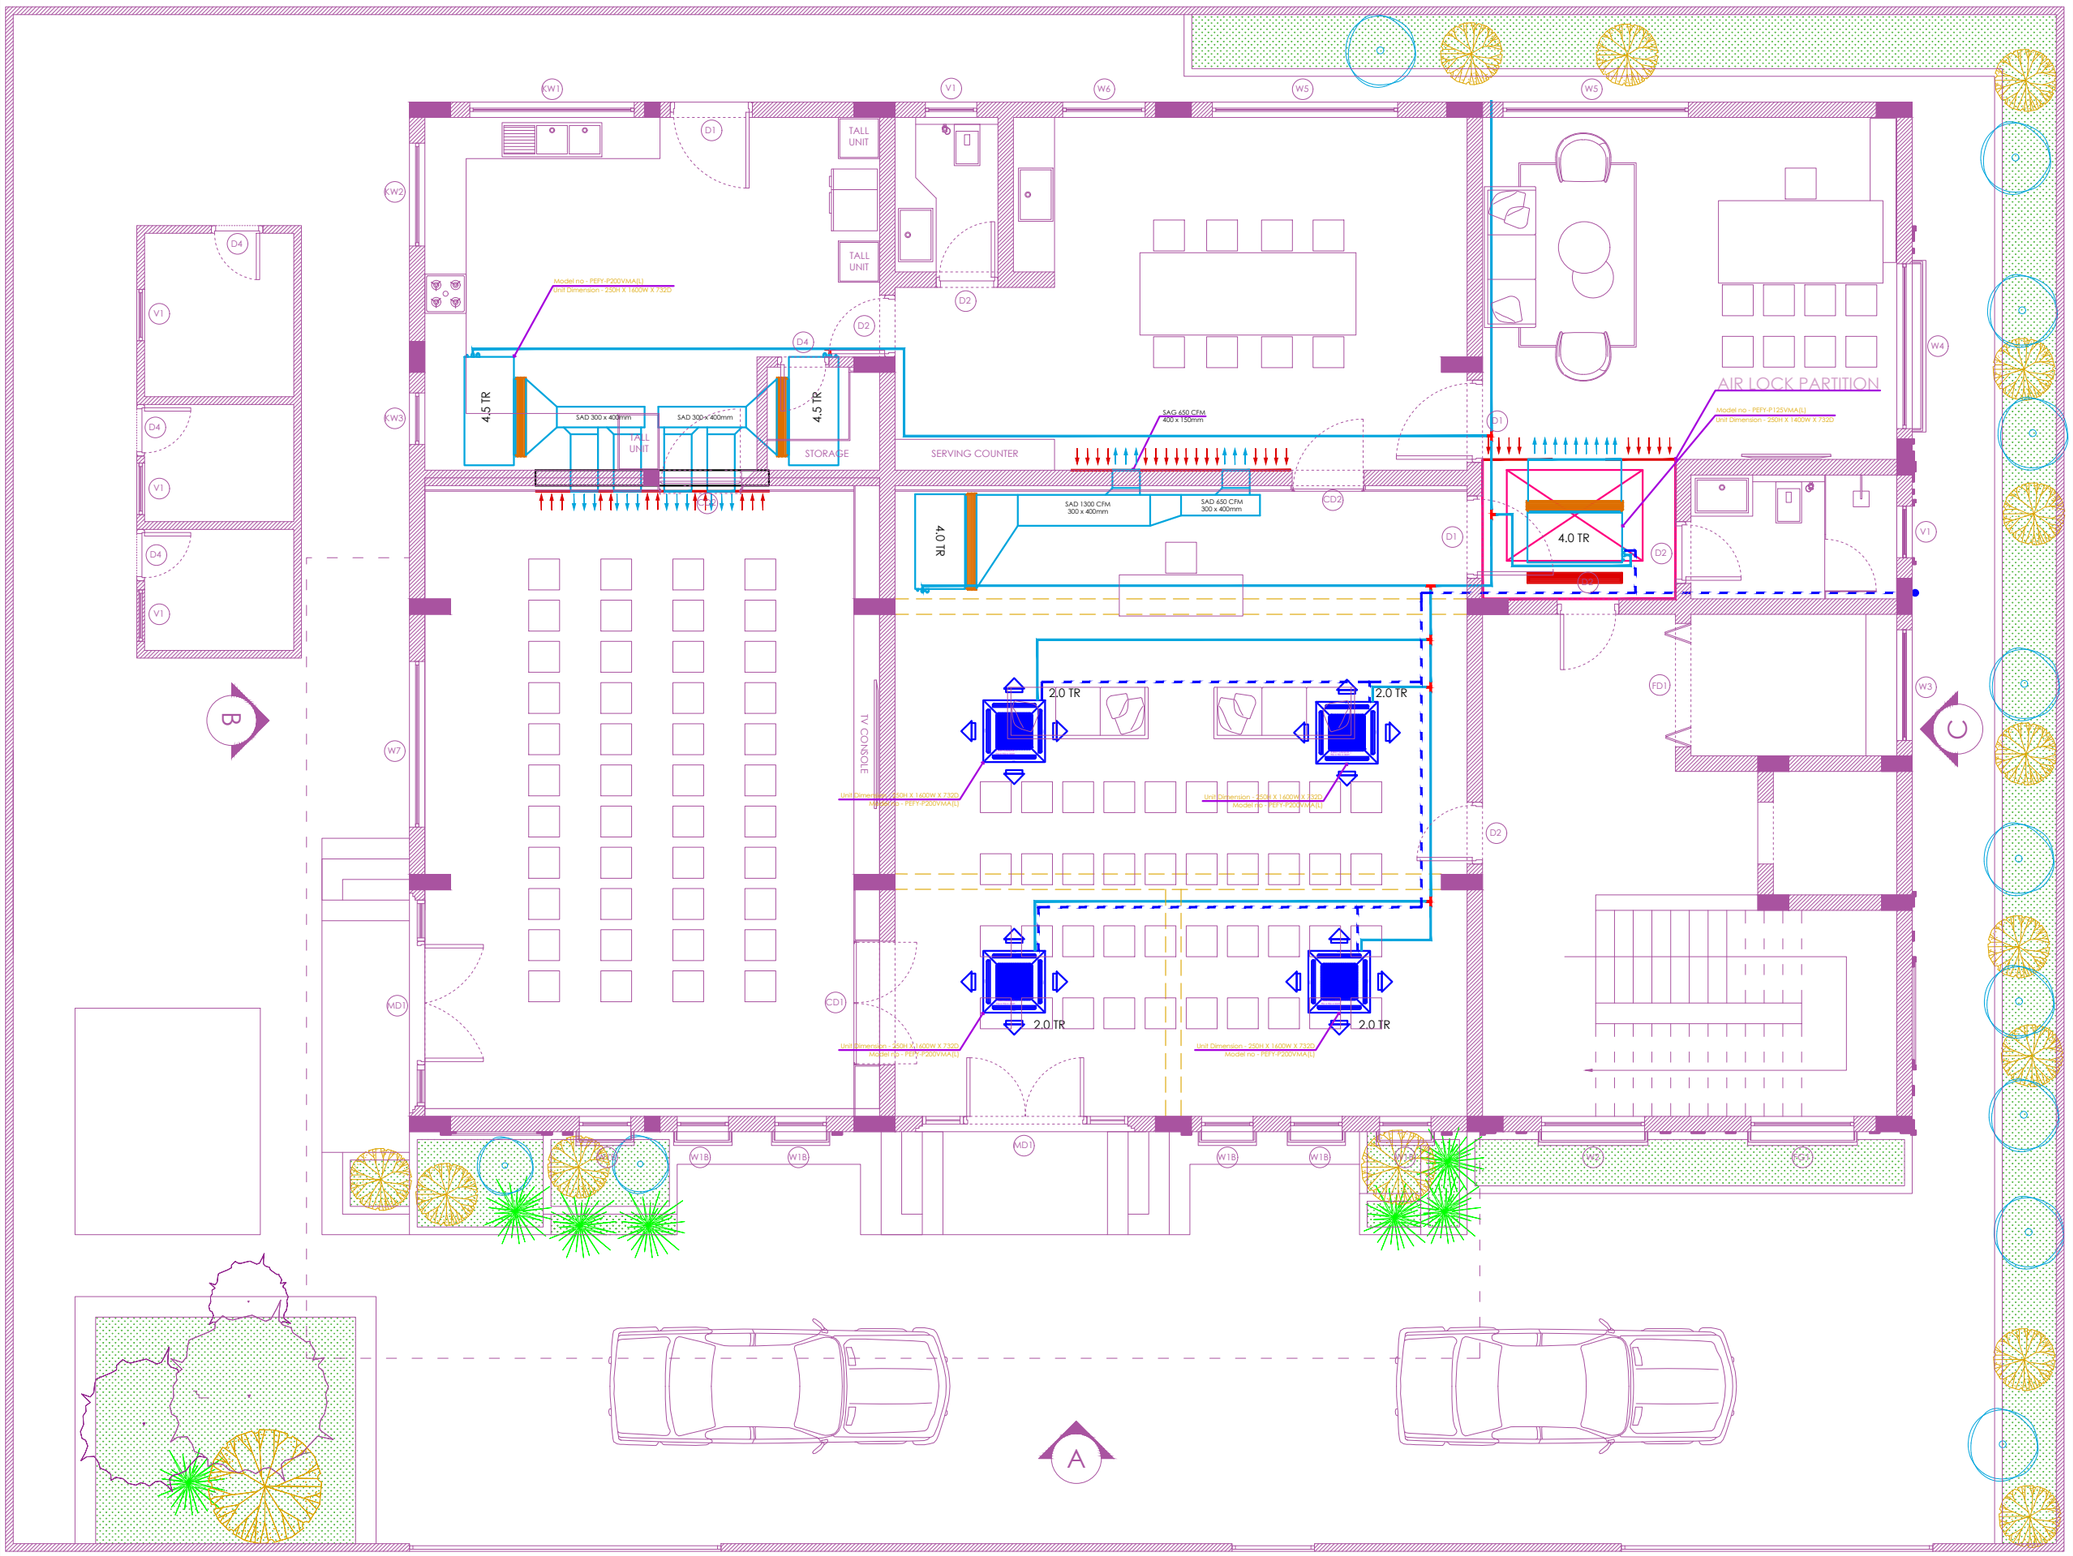


SITE PLAN :

NOTE :

PROJECT :

VILLA

SR NO	DATE	DESCRIPTIONS	DRWN BY
		ISSUED FOR APPROVAL	


CLIENT :

MAIN CONTRACTOR :

MEP CONSULTANT:

BenderZ Design & Consultant

PROJECT NO:		
DRAWING TITLE: GROUND FLOOR-HVAC SHOP DRAWING- VRV		
DRAWING NO :		DATE:
DRAWN BY:	CHECKED BY:	SCALE:
SERIAL NO:	SHEET NO:	REV.NO:

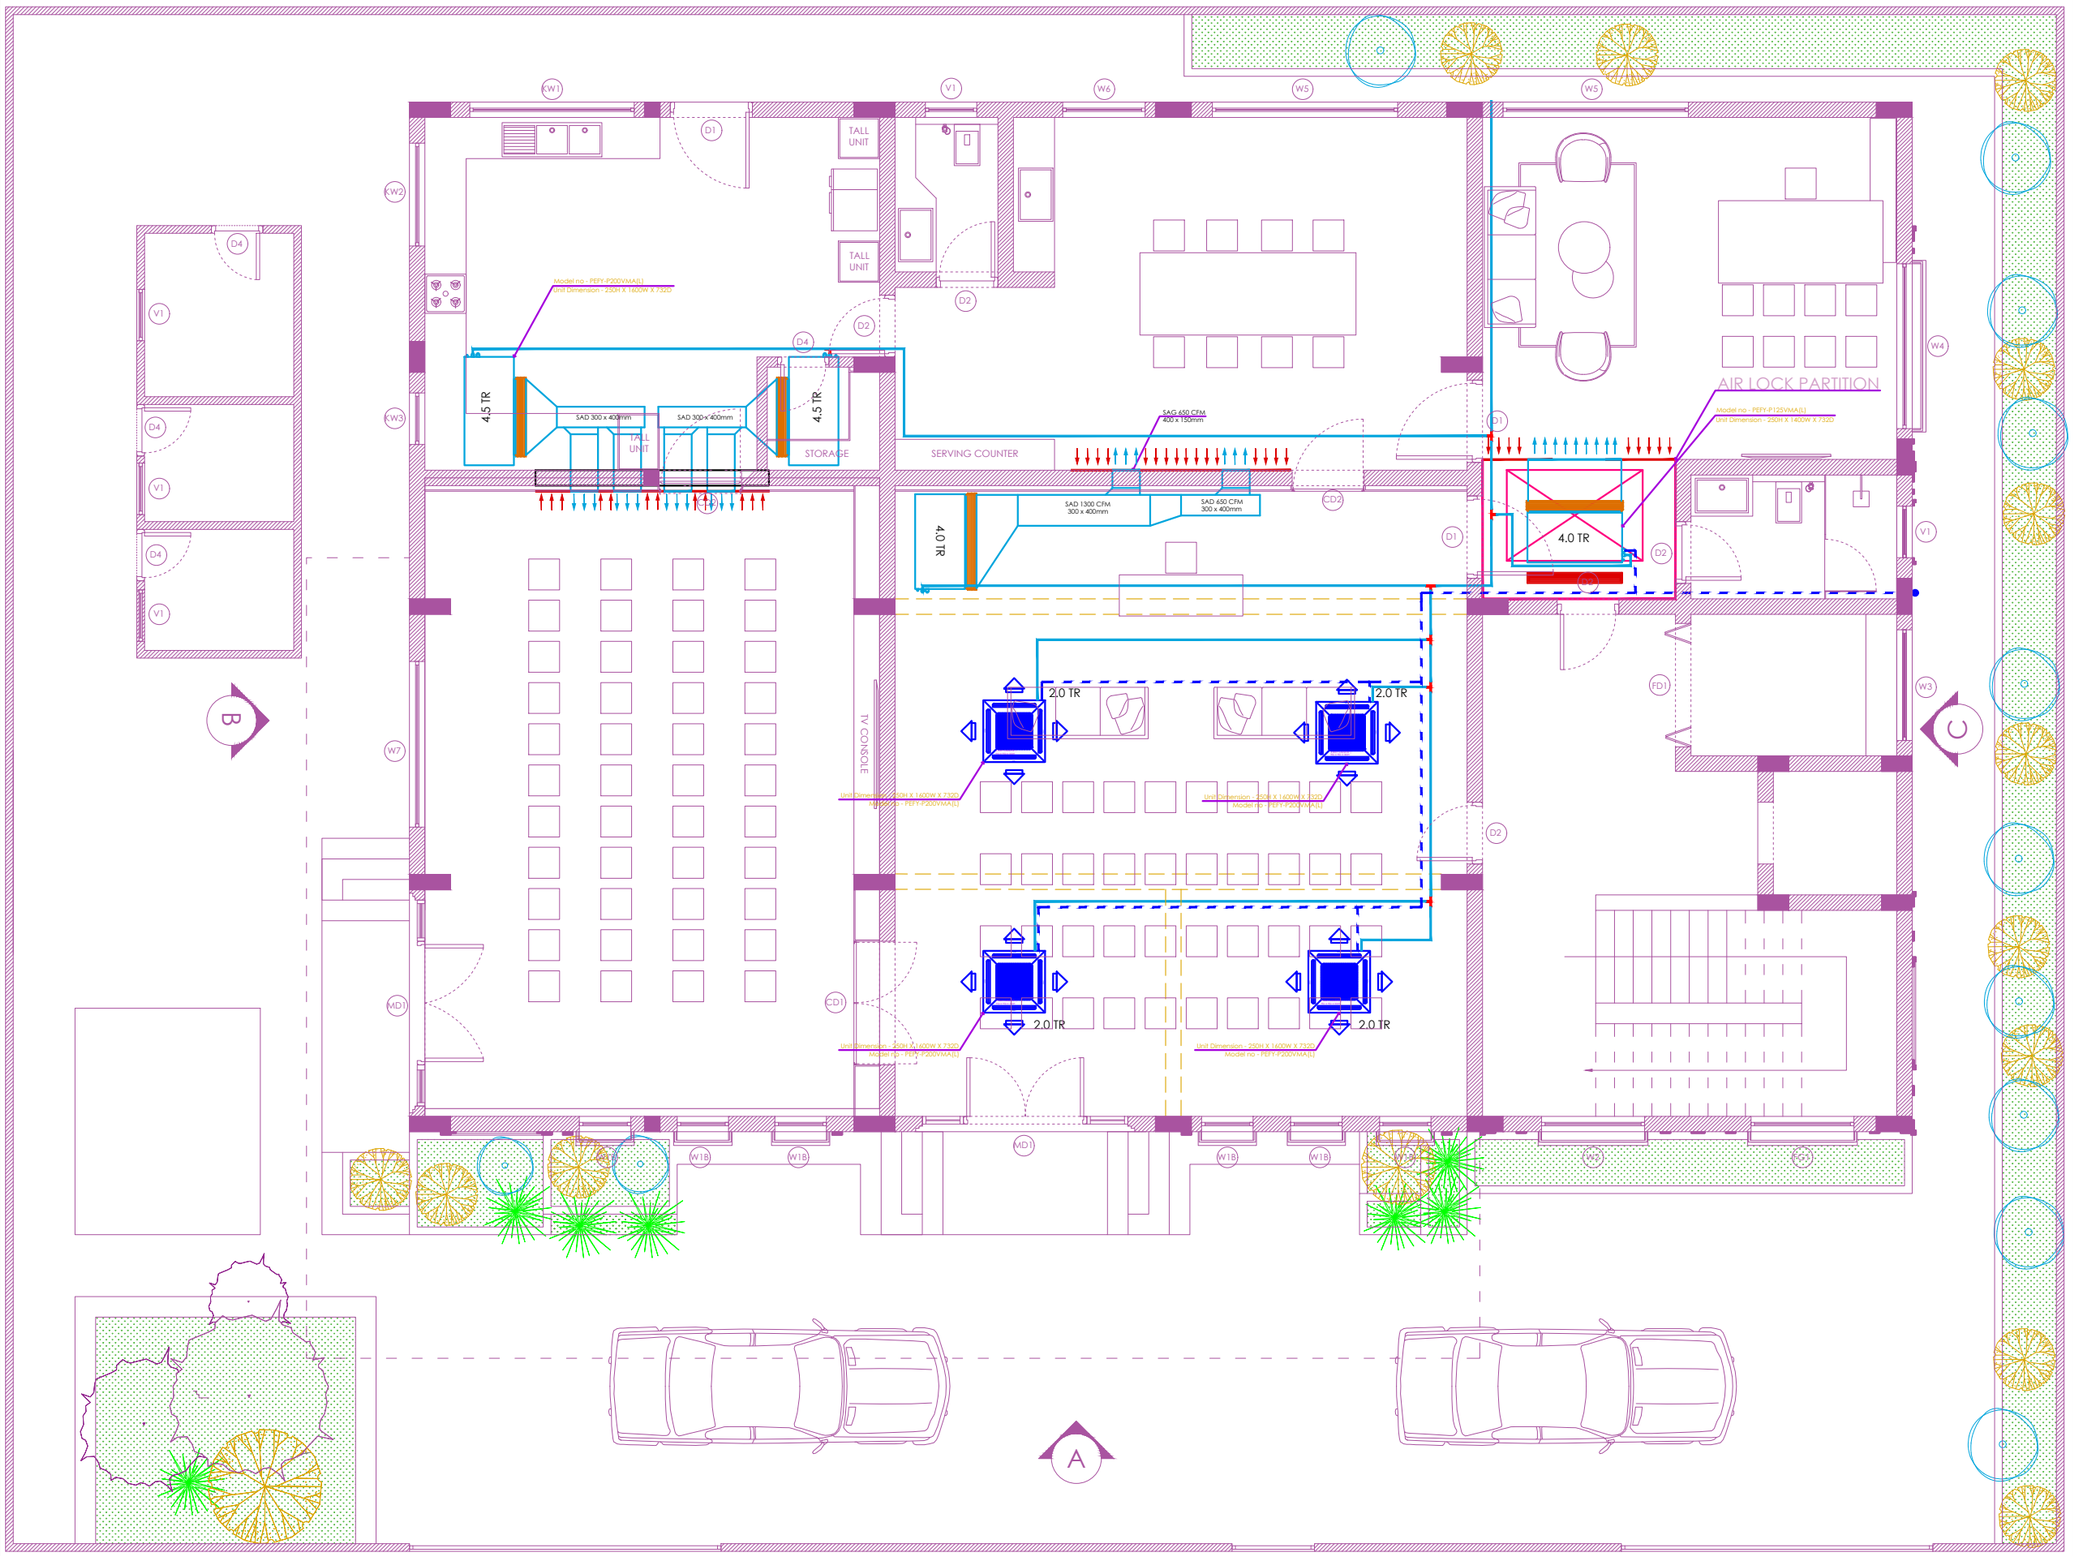

SITE PLAN :

NOTE :

PROJECT :

VILLA

SR NO	DATE	DESCRIPTIONS	DRWN BY
		ISSUED FOR APPROVAL	


CLIENT :

MAIN CONTRACTOR :

MEP CONSULTANT:

BenderZ Design & Consultant

PROJECT NO:		
DRAWING TITLE: FIRST FLOOR-HVAC SHOP DRAWING- VRV		
DRAWING NO :		DATE:
DRAWN BY:	CHECKED BY:	SCALE:
SERIAL NO:	SHEET NO:	REV.NO:

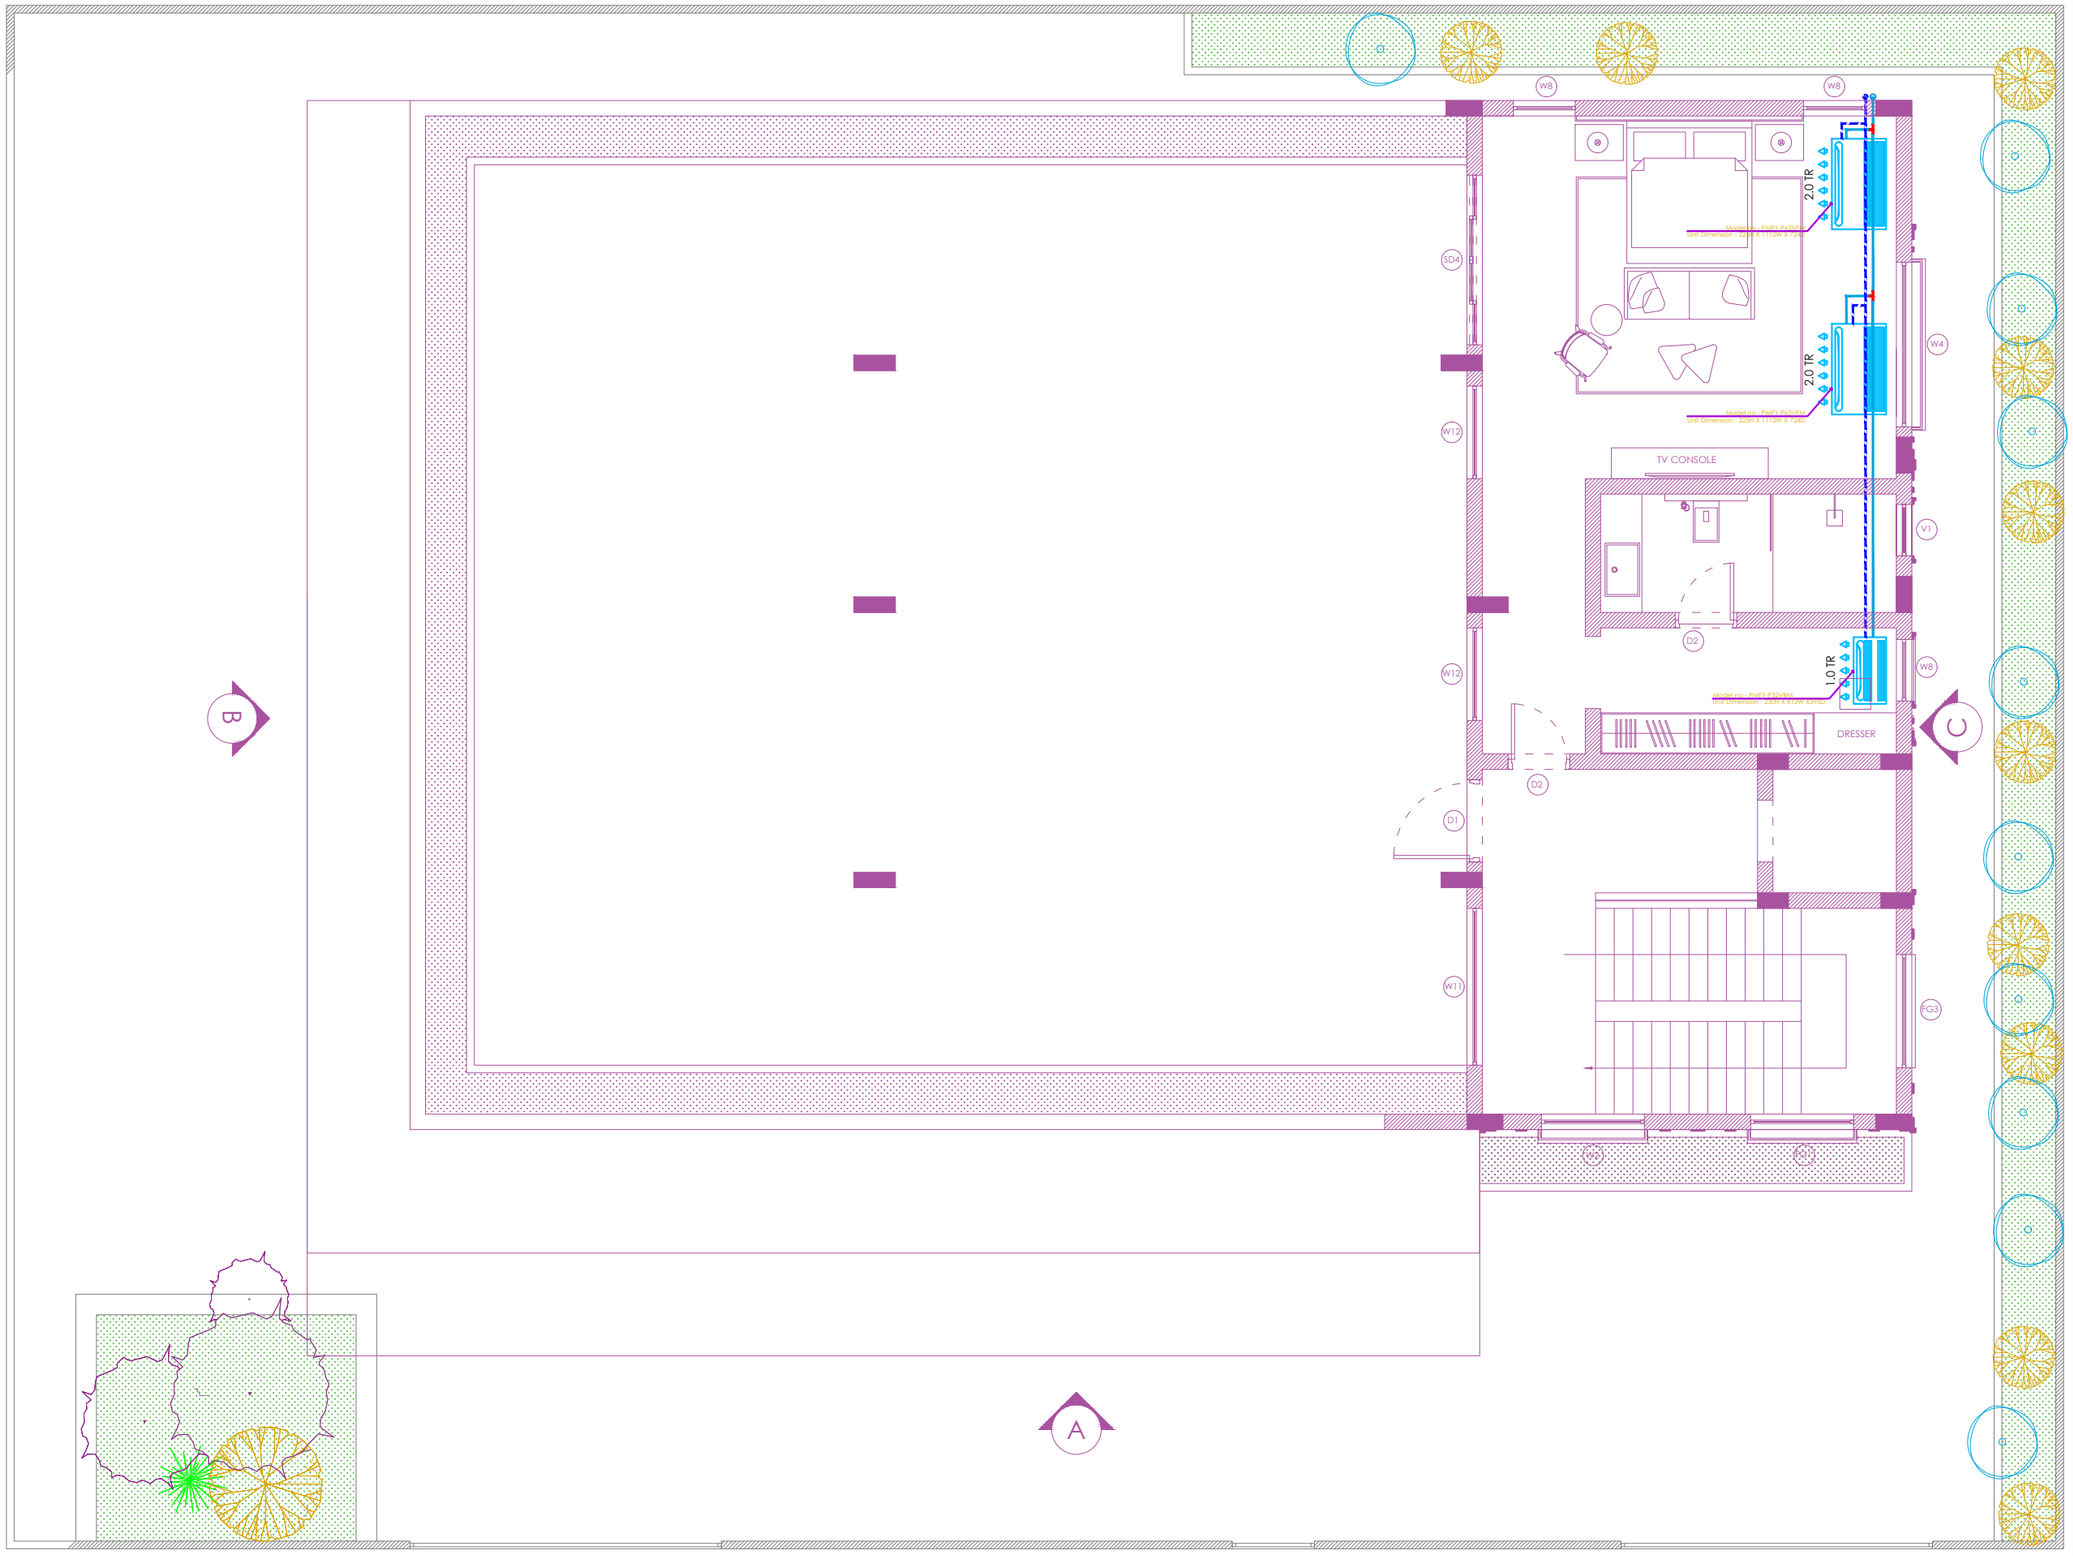

SITE PLAN :

NOTE :

PROJECT :

VILLA

SR NO	DATE	DESCRIPTIONS	DRWN BY
		ISSUED FOR APPROVAL	


CLIENT :

MAIN CONTRACTOR :

MEP CONSULTANT:

BenderZ Design & Consultant

PROJECT NO:		
DRAWING TITLE: SECOND FLOOR-HVAC SHOP DRAWING- VRV		
DRAWING NO :		DATE:
DRAWN BY:	CHECKED BY:	SCALE:
SERIAL NO:	SHEET NO:	REV.NO:

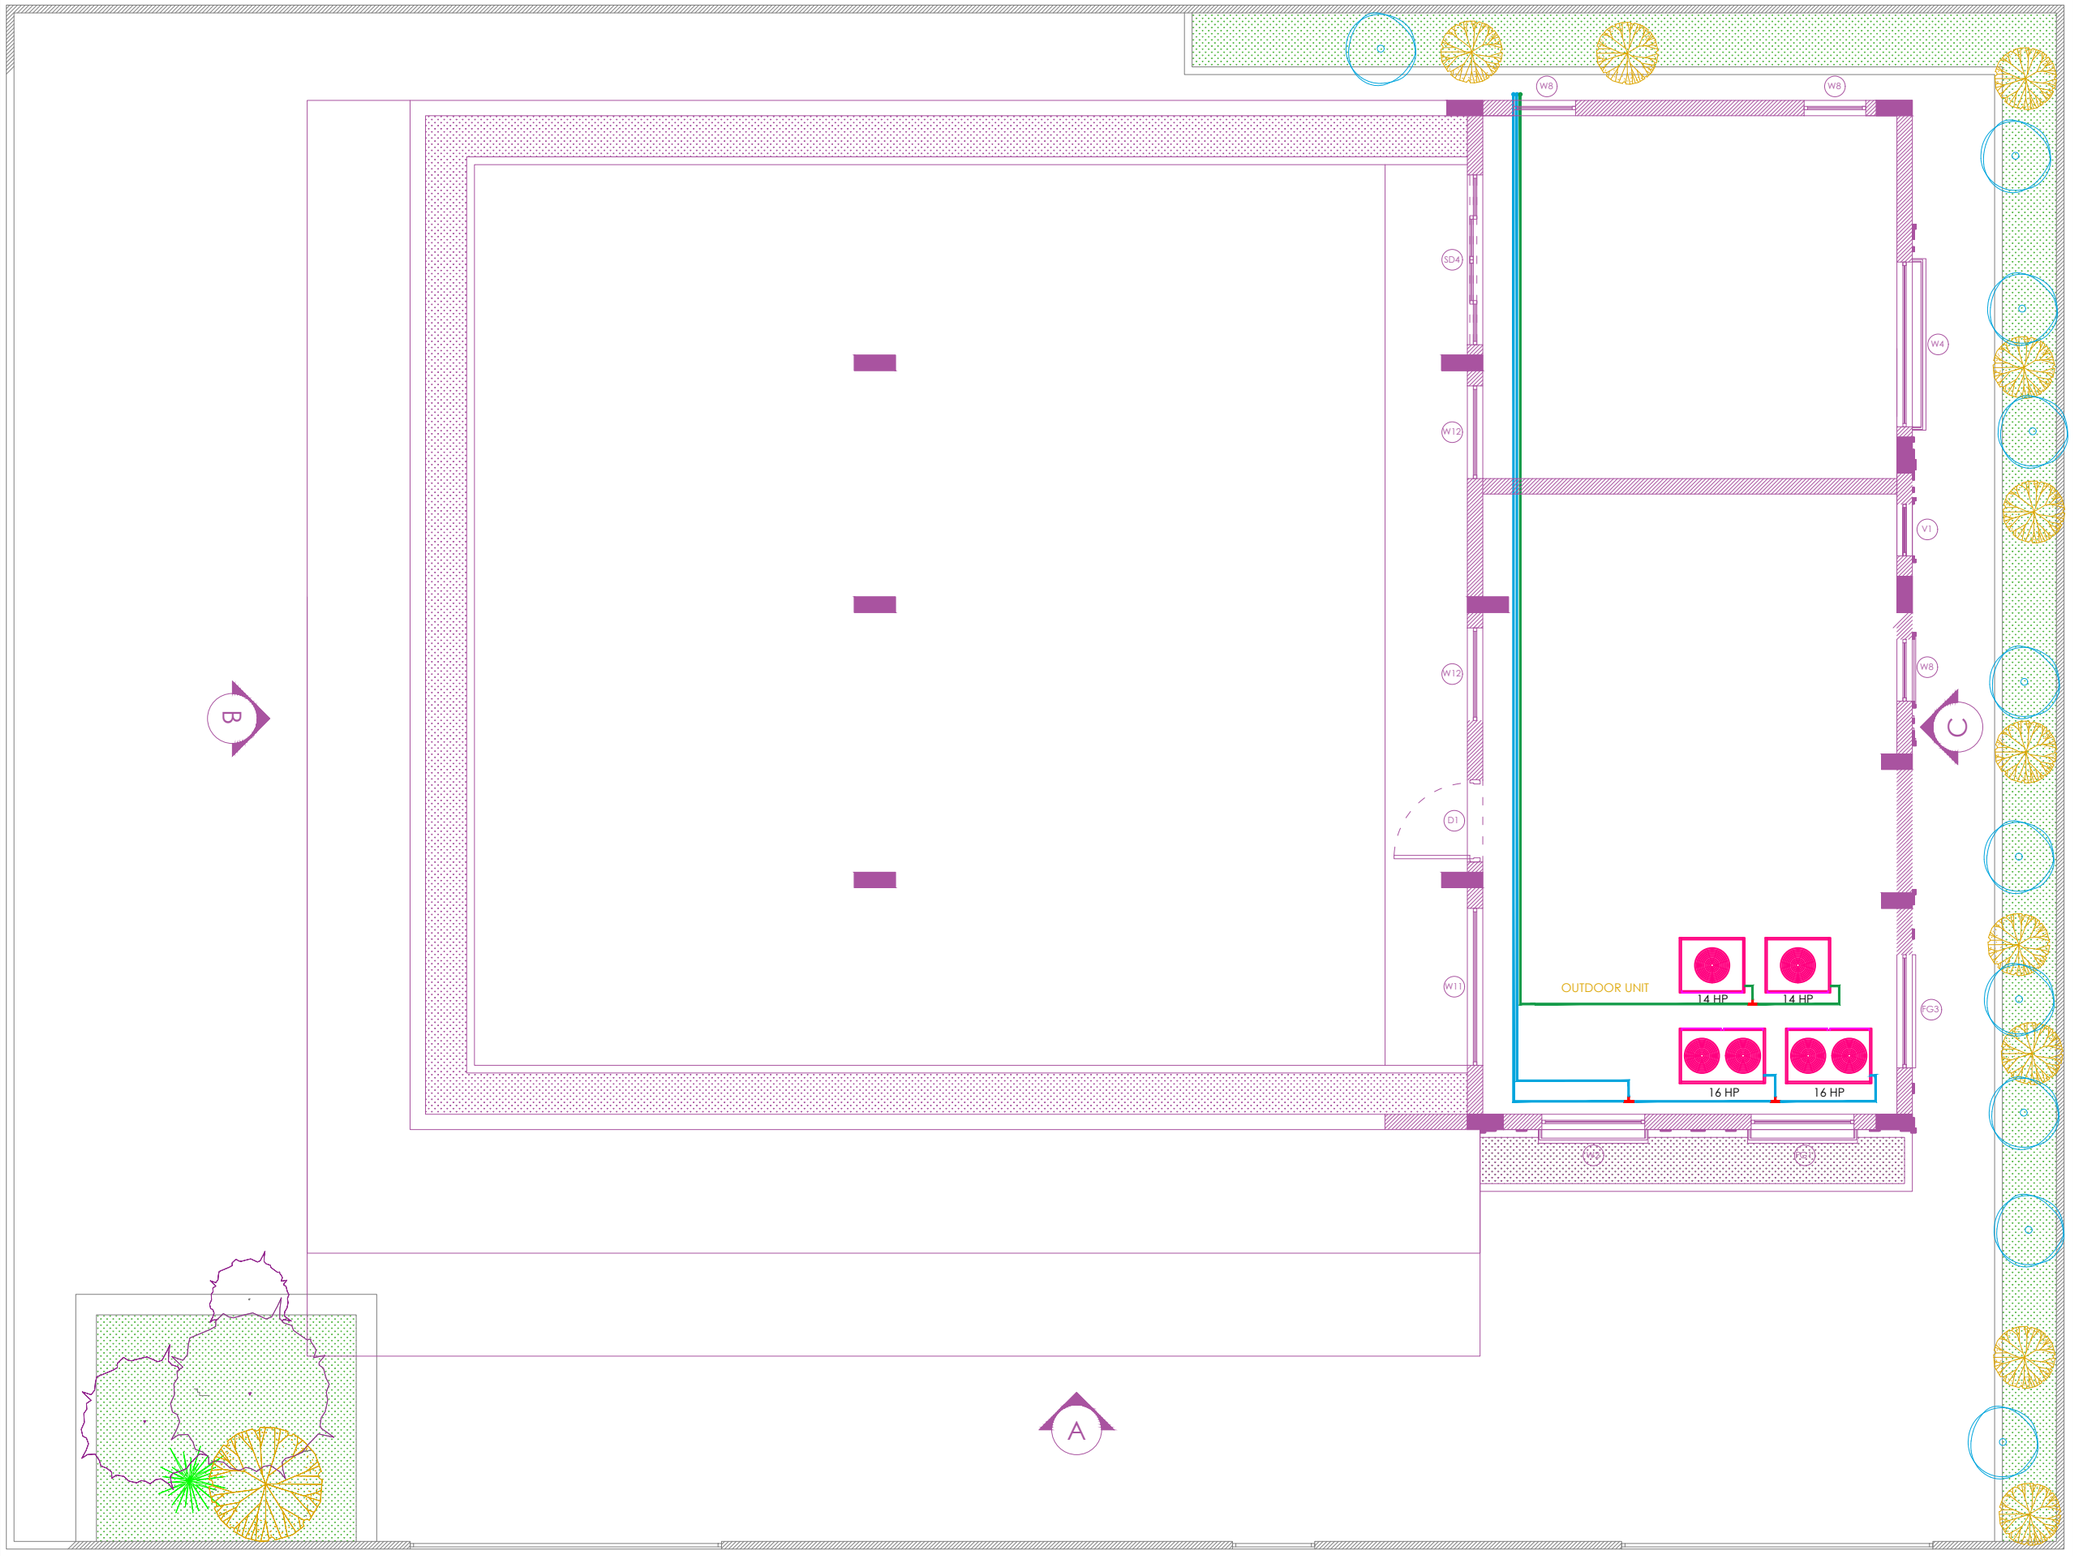

SITE PLAN :

NOTE :

PROJECT :

VILLA

SR NO	DATE	DESCRIPTIONS	DRWN BY
		ISSUED FOR APPROVAL	

CLIENT :

MAIN CONTRACTOR :

MEP CONSULTANT:

BenderZ Design & Consultant

PROJECT NO:		
DRAWING TITLE: TERRACE FLOOR-HVAC SHOP DRAWING- VRV		
DRAWING NO :		DATE:
DRAWN BY:	CHECKED BY:	SCALE:
SERIAL NO:	SHEET NO:	REV.NO: