
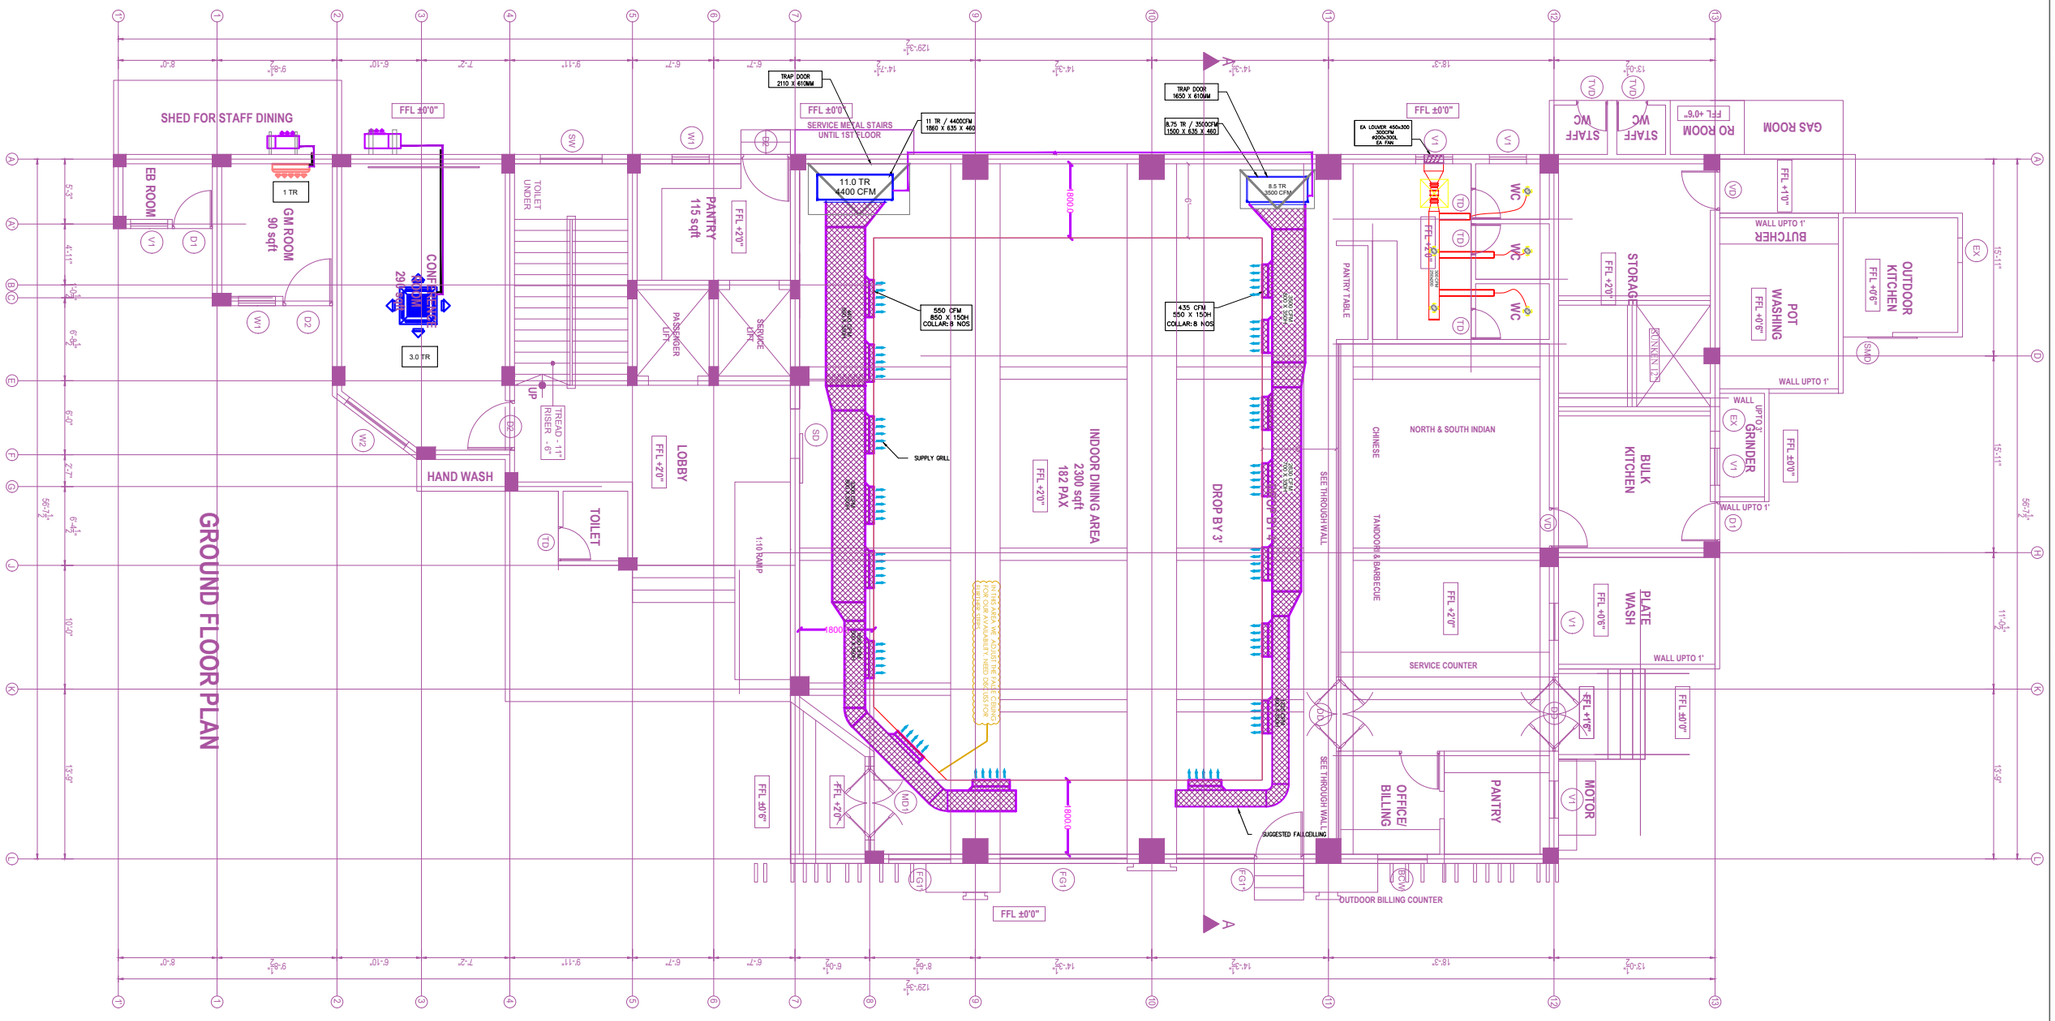


SITE PLAN :

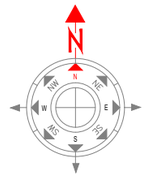

NOTE :

PROJECT :

RESTAURANT

SR NO	DATE	DESCRIPTIONS	DRWN BY
		ISSUED FOR APPROVAL	


CLIENT :

MAIN CONTRACTOR :


MEP CONSULTANT:

BenderZ Design & Consultant

PROJECT NO:		
DRAWING TITLE: GROUND FLOOR - HVAC SHOP DRAWING		
DRAWING NO :		DATE:
DRAWN BY:	CHECKED BY:	SCALE:
SERIAL NO:	SHEET NO:	REV.NO:

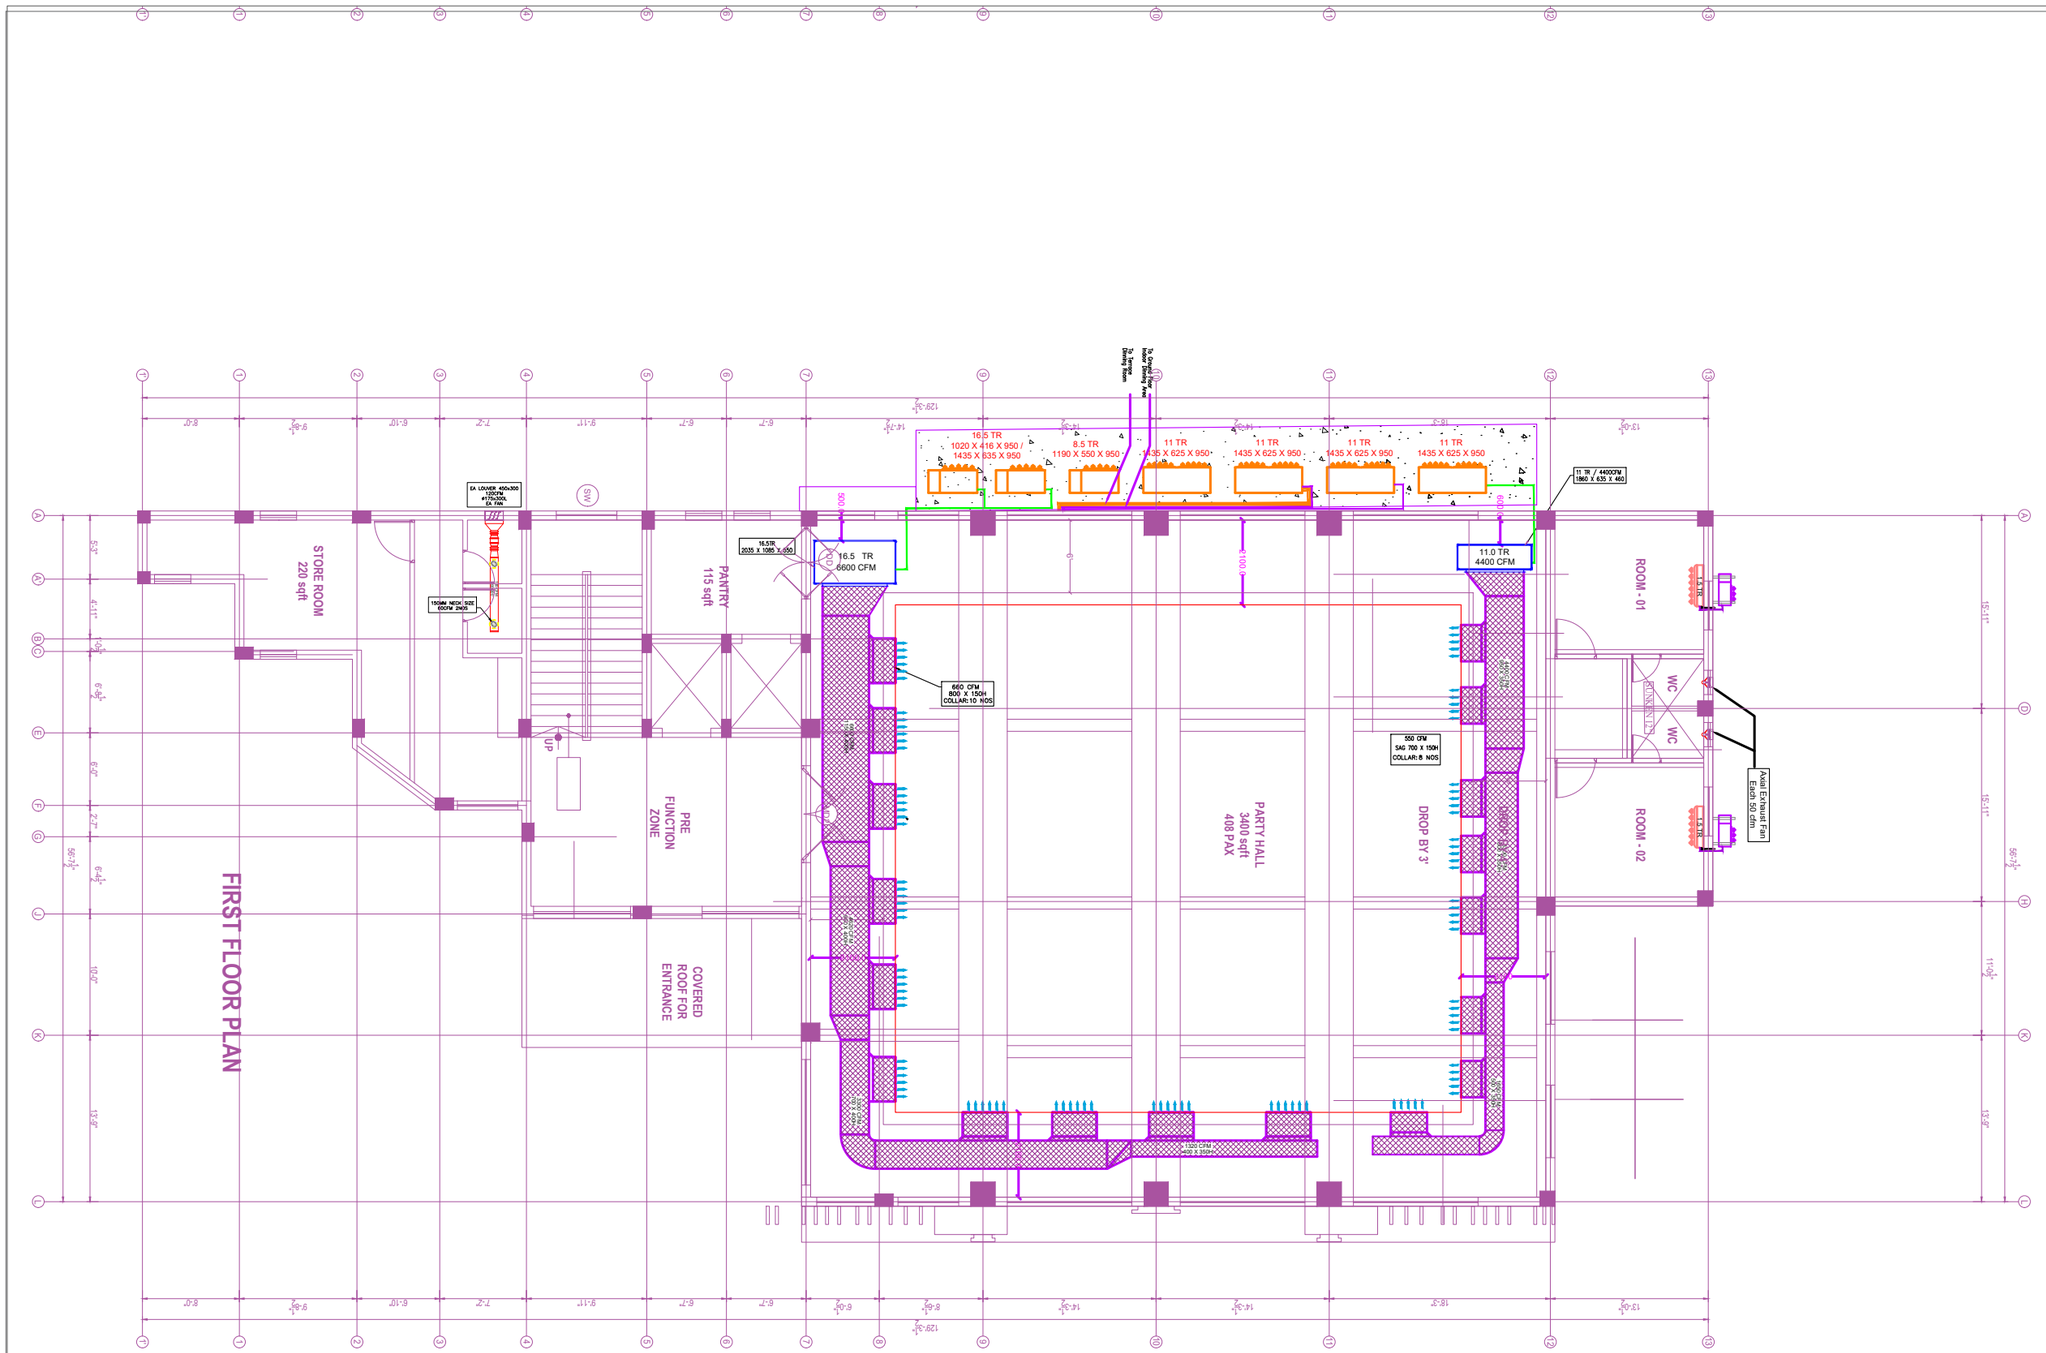

SITE PLAN :

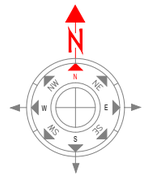

NOTE :

PROJECT :

RESTAURANT

SR NO	DATE	DESCRIPTIONS	DRWN BY
		ISSUED FOR APPROVAL	


CLIENT :

MAIN CONTRACTOR :


MEP CONSULTANT:

BenderZ
Design & Consultant

PROJECT NO:		
DRAWING TITLE: FIRST FLOOR - HVAC SHOP DRAWING		
DRAWING NO :		DATE:
DRAWN BY:	CHECKED BY:	SCALE:
SERIAL NO:	SHEET NO:	REV.NO:

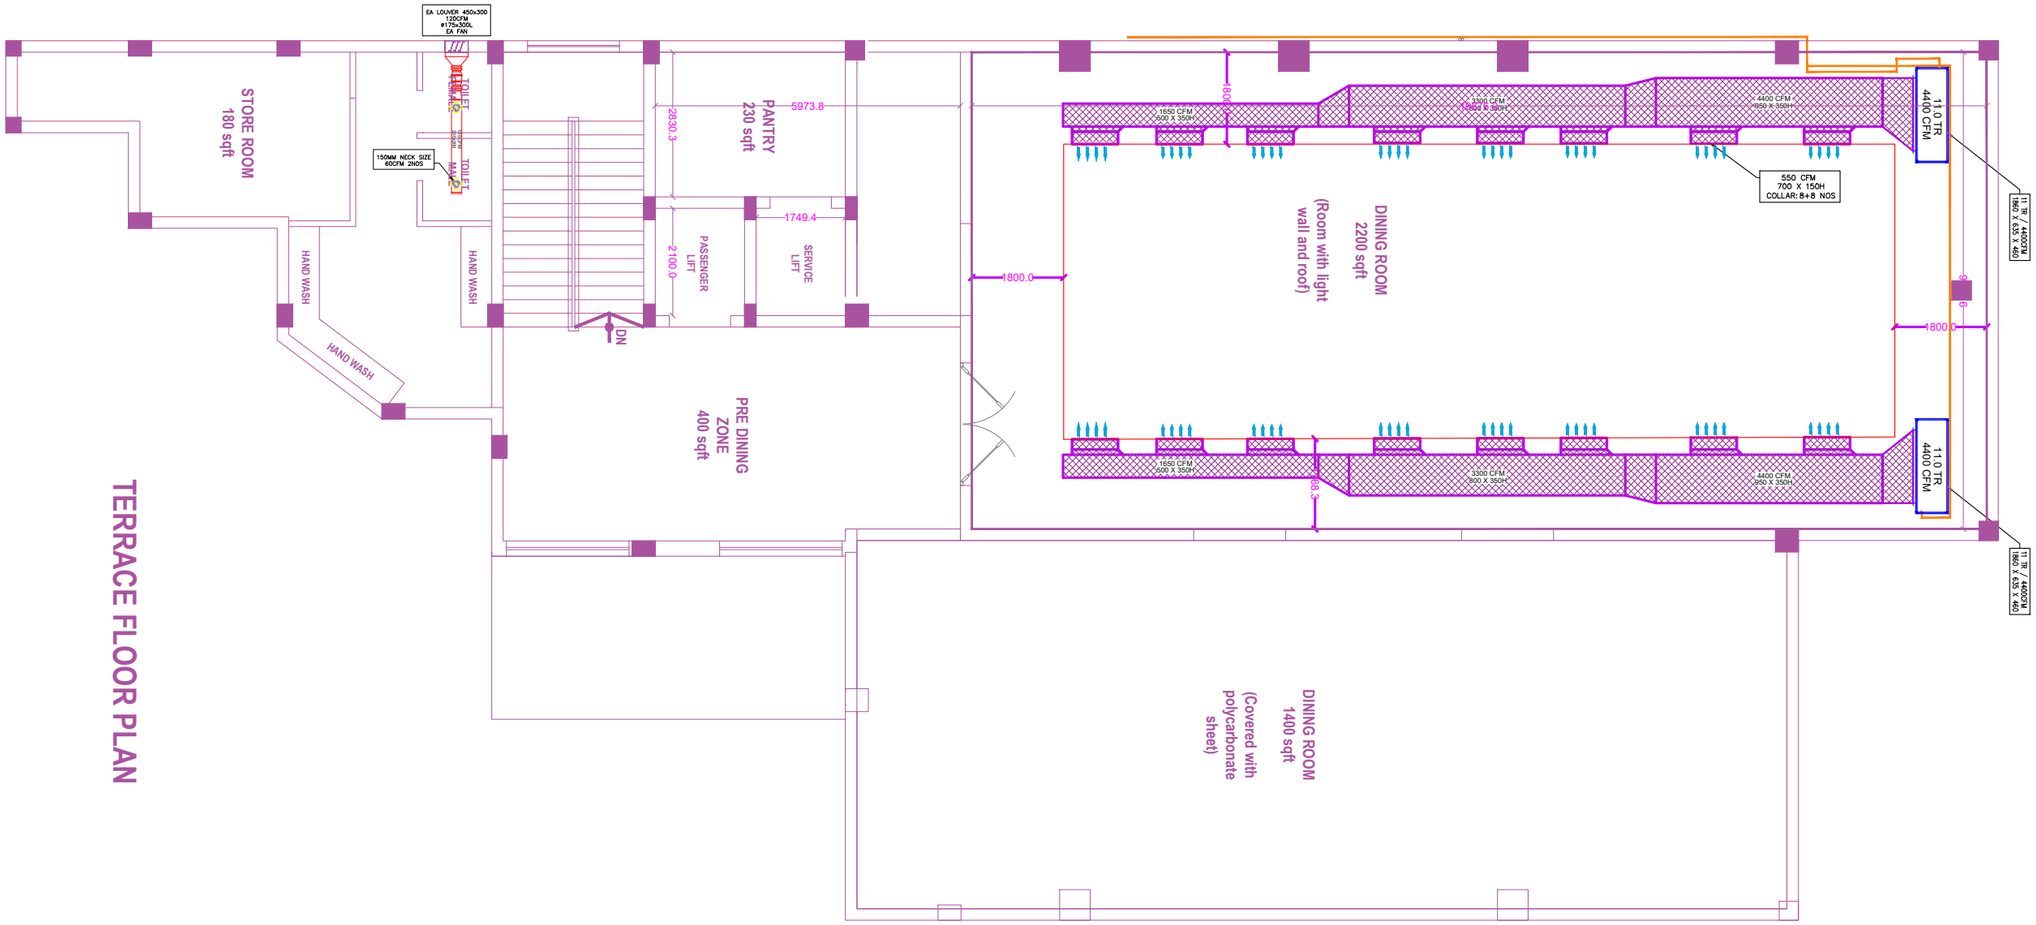

SITE PLAN :

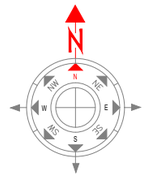

NOTE :

PROJECT :

RESTAURANT

SR NO	DATE	DESCRIPTIONS	DRWN BY
		ISSUED FOR APPROVAL	

CLIENT :

MAIN CONTRACTOR :

MEP CONSULTANT:

BenderZ
Design & Consultant

PROJECT NO:		
DRAWING TITLE: SECOND FLOOR - HVAC SHOP DRAWING		
DRAWING NO :		DATE:
DRAWN BY:	CHECKED BY:	SCALE:
SERIAL NO:	SHEET NO:	REV.NO: