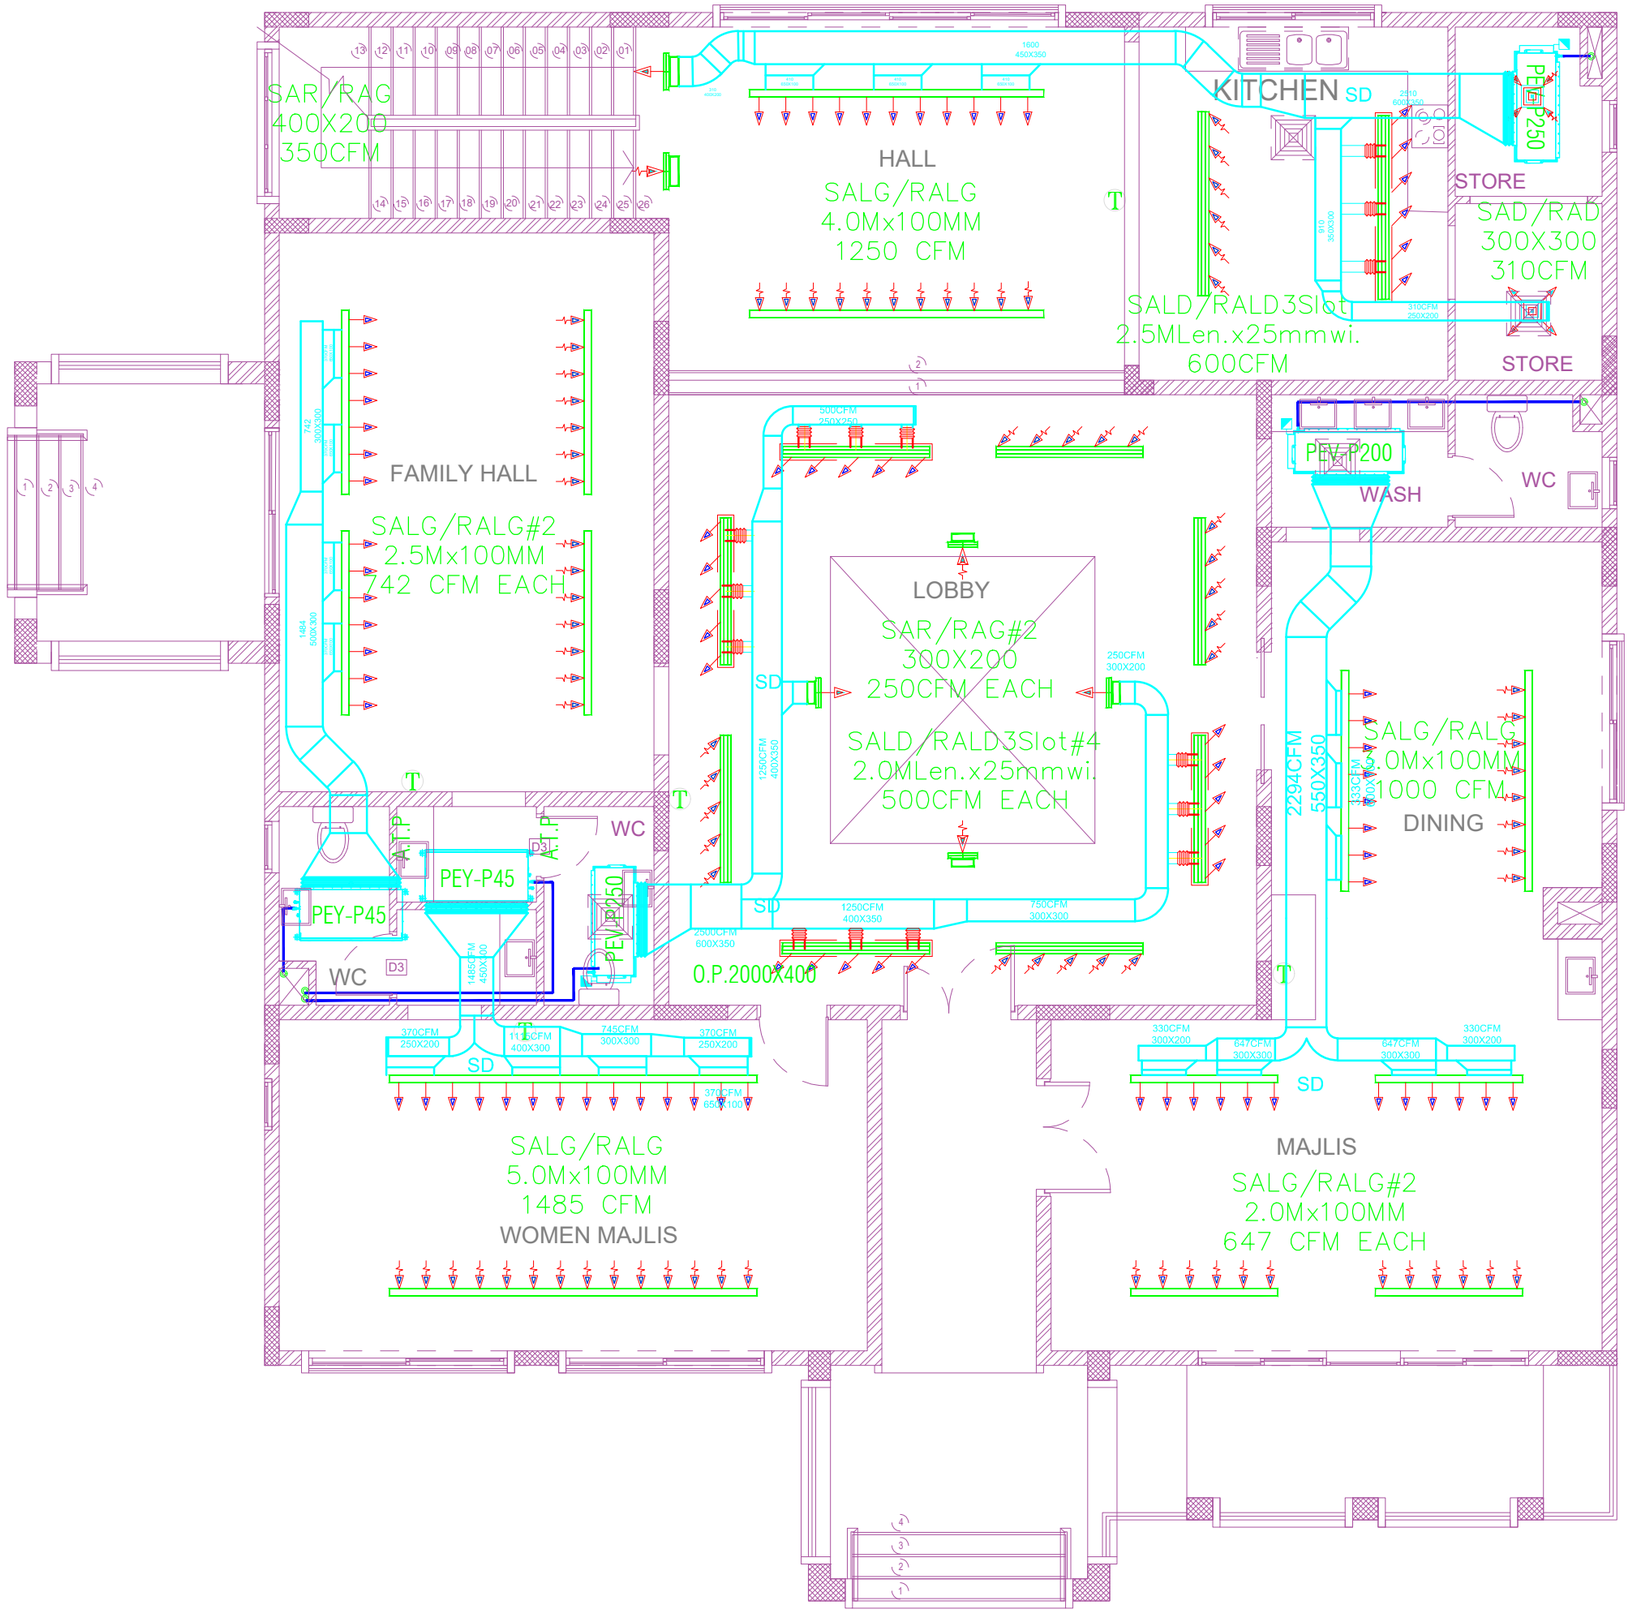


SITE PLAN :

NOTE :

PROJECT :

VILLA - DUBAI

SR NO	DATE	DESCRIPTIONS	DRWN BY
		ISSUED FOR APPROVAL	

CLIENT :

MAIN CONTRACTOR :

MEP CONSULTANT:

BenderZ Design & Consultant

PROJECT NO:		
DRAWING TITLE: VILLA-HVAC DUCT DRAWING		
DRAWING NO :		DATE:
DRAWN BY:	CHECKED BY:	SCALE:
SERIAL NO:	SHEET NO:	REV.NO: