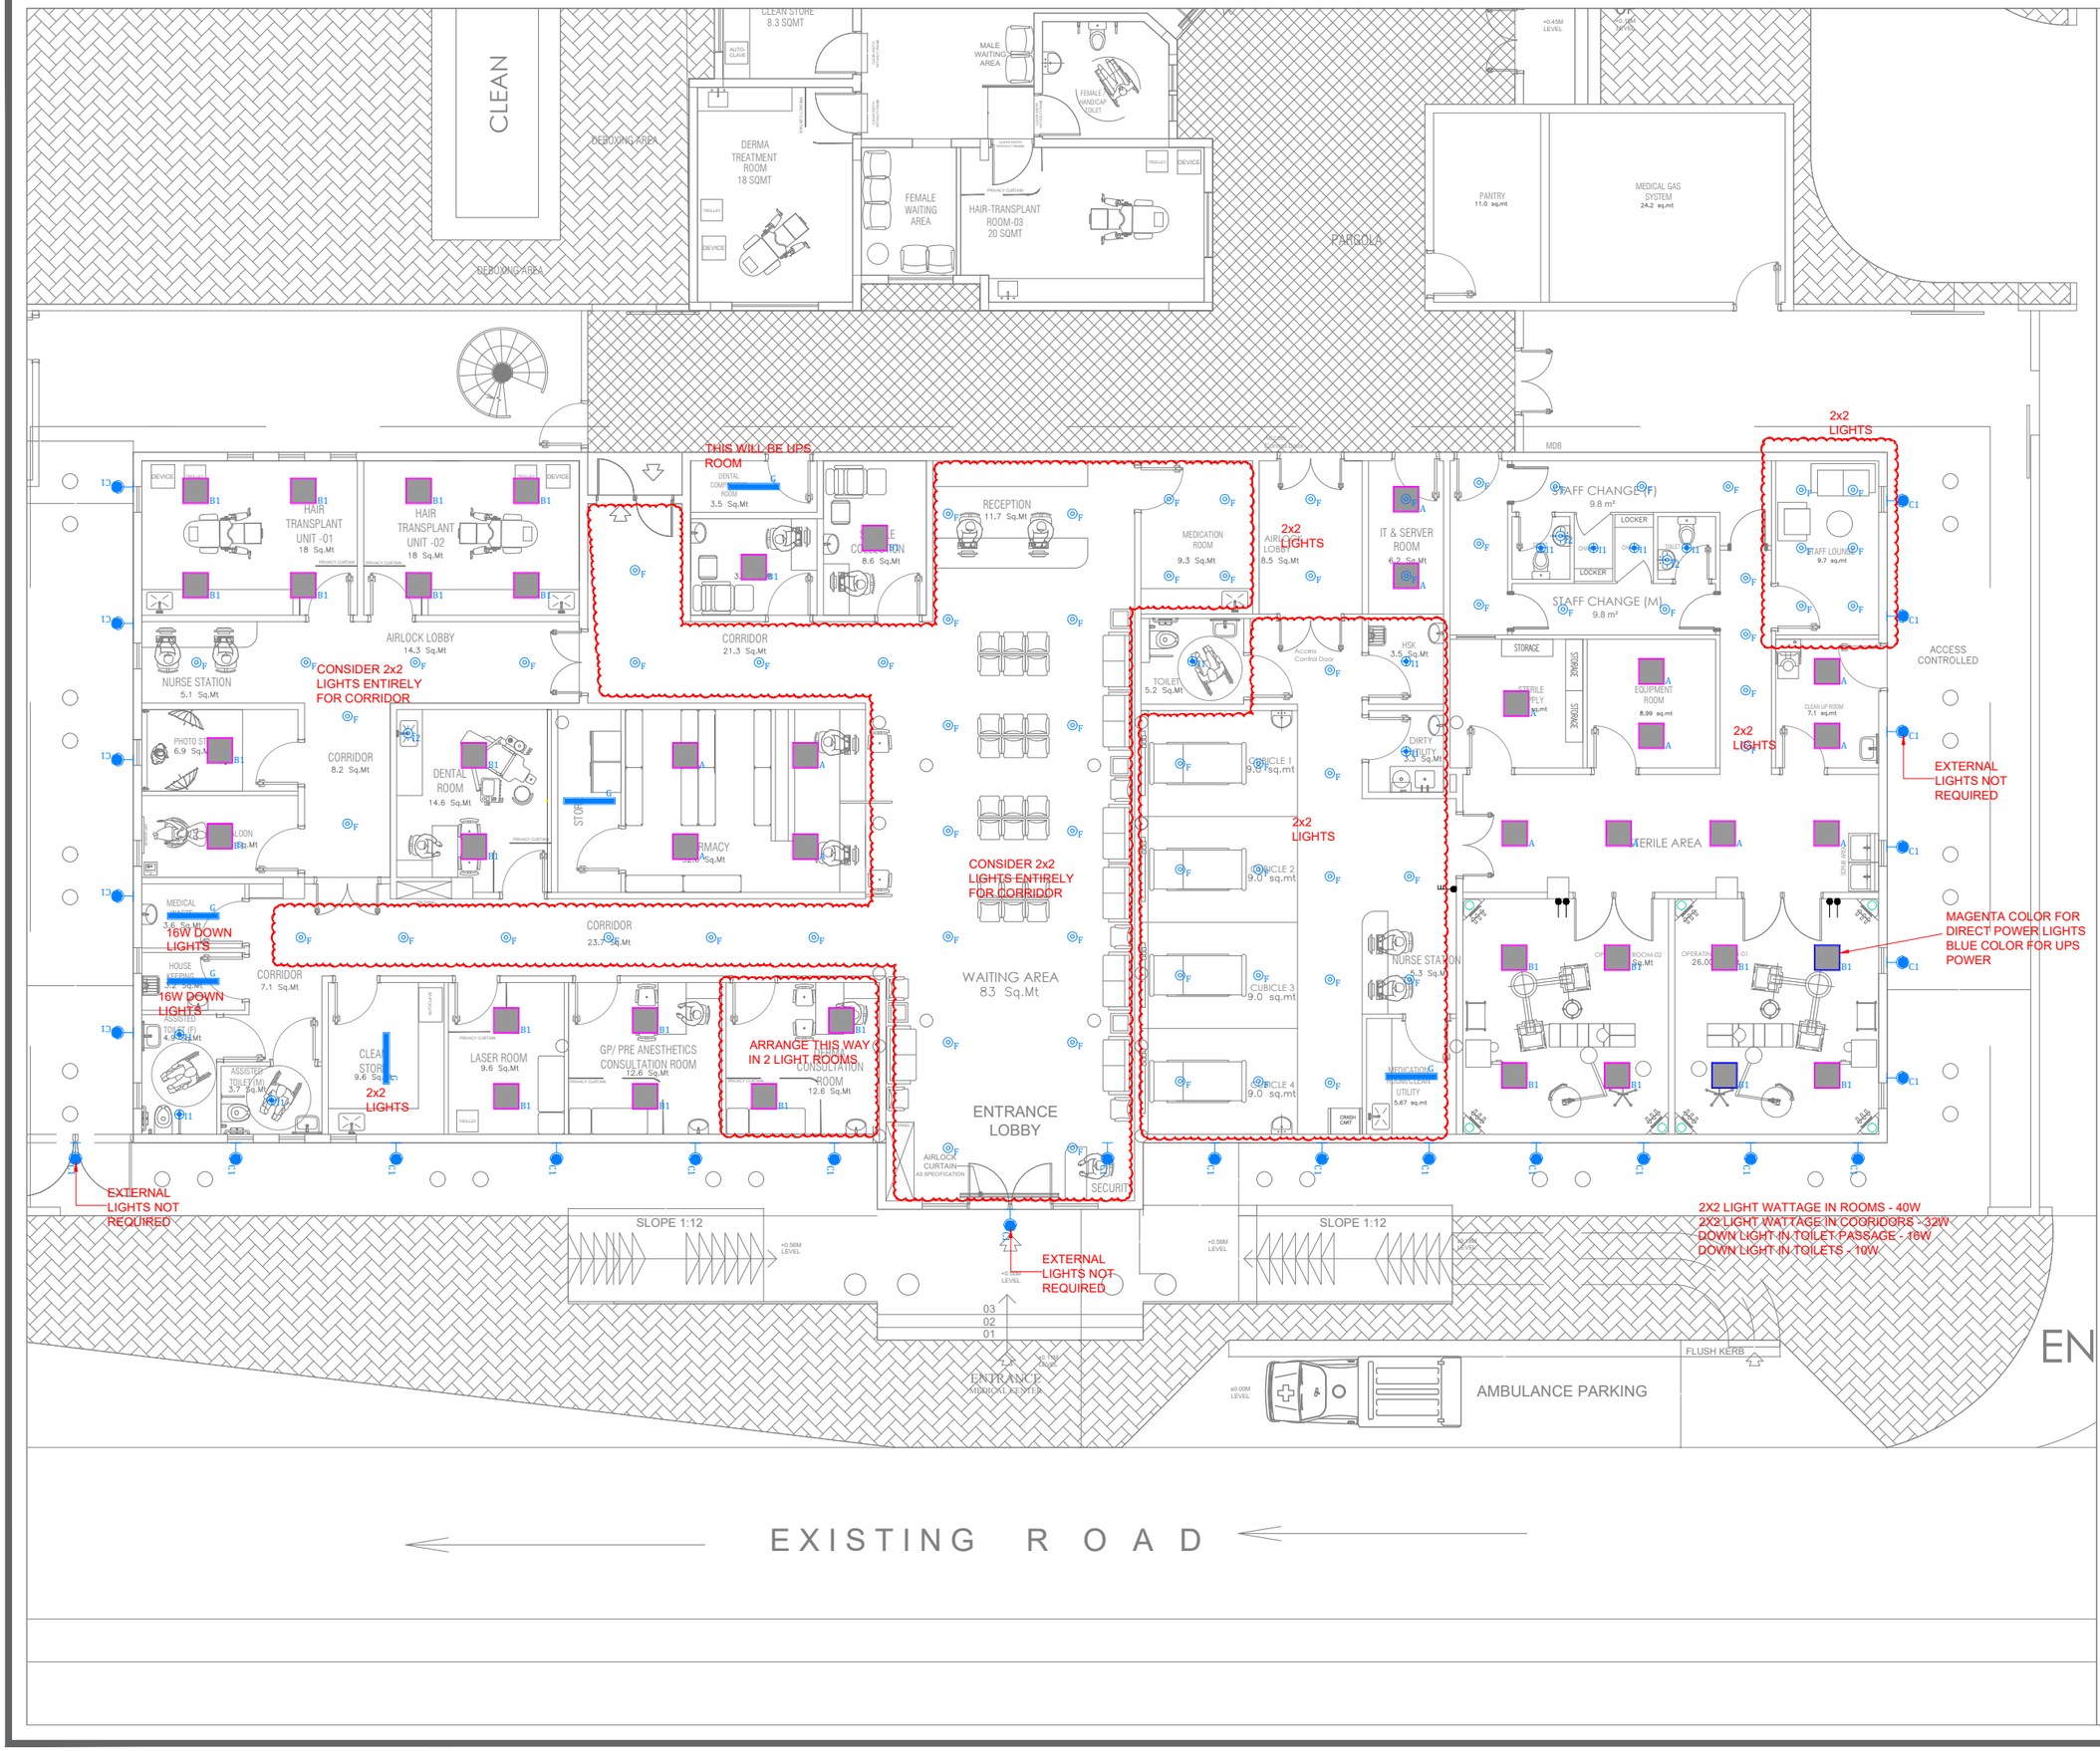


LIGHTING ILLUMINATION LEGENDS:

SYMBOL	DESCRIPTION	MOUNTING HEIGHT
	10A SP ONE GANG ONE WAY SWITCH.	1200mm AFFL
	10A SP TWO GANG ONE WAY SWITCH.	1200mm AFFL
	10A SP THREE GANG ONE WAY SWITCH.	1200mm AFFL
	10A SP ONE GANG TWO WAY SWITCH.	1200mm AFFL
	10A SP TWO GANG TWO WAY SWITCH.	1200mm AFFL
	16A DIMMER SWITCH WITH ON/OFF CONTROL	1200mm AFFL
	16A SP BELL PUSH.	1200mm AFFL
	PUSH BUTTON SWITCH FOR STAIRCASE.	1200mm AFFL
	OVERRIDE SWITCH.	1200mm AFFL
A	29W LED 600x600 TILE LIGHT, 3600LUMENS.	
A1	29W LED 600x600 DIMMER, TILE LIGHT, 3600LUMENS.	
B	34.5W LED 600x600 LIGHT FUXTURE, 4300 LUMENS, IP-20/44.	
B1	34.5W LED 600x600 DIMMER LIGHT FUXTURE, 4300 LUMENS, IP-20/44.	
C	15W SURFACE MOUNTED LED SUITABLE FOR EXTERNAL PARAPET INSTALLATIONS, IP-65.	
C1	15W SURFACE MOUNTED LED SUITABLE ,IP-44.	
D	1 x E27, 23W, LED, 230V-50HZ BULK HEAD FITTING, DIE CAST ALUMINIUM HOUSING, GLASS DIFFUSER, IP44 (FOR STAIR).	
E	33W LED 600x600 LIGHT FUXTURE, 4377 LUMENS, IP-20/44.	
F	16.8W LED DOWN LIGHT FUXTURE, 2200 LUMENS, 4000K, IP-20.	
G	42.9W LED LIGHT FUXTURE, 6000 LUMENS, 4000K, IP-65.	
H	150W LED HIGH BAY LUMINAIRE, ROBUST DIE-CAST HOUSING WITH INTEGRATED COOLING RIBS, 4000K, 152LM/W, IP-65.	
I1	9.4W LED DOWN LIGHT FUXTURE, 101LM/W, 4000K, IP-44.	
I2	8W LED SPOT LIGHT FUXTURE, 4000K, IP-44.	
J	SURFACE MOUNTED FLUORESCENT LIGHT FIXTURE WITH 2x36W T8 LAMP, IP-20.	
J1	2x21W LED SURFACED/WALL LIGHT FIXTURE 7200-LUMENS, COLOR TEMPERATURE-4000K IP-65 (FOR SUBSTATION & RMU ROOM).	
K	8W LED BULK HEAD LIGHT, IP-65.	
	STANDALONE MOTION SENSOR.	
LCP	LIGHTING CONTROL PANEL.	

PROJECT :

Multi Speciality Hospital

SR NO	DATE	DESCRIPTIONS	DRWN BY
		ISSUED FOR APPROVAL	


CLIENT :

MAIN CONTRACTOR :

MEP CONSULTANT:

BenderZ Design & Consultant

PROJECT NO:		
DRAWING TITLE: GROUND FLOOR - ELECTRICAL- LIGHT LOAD		
DRAWING NO :		DATE:
DRAWN BY:	CHECKED BY:	SCALE:
SERIAL NO:	SHEET NO:	REV.NO:

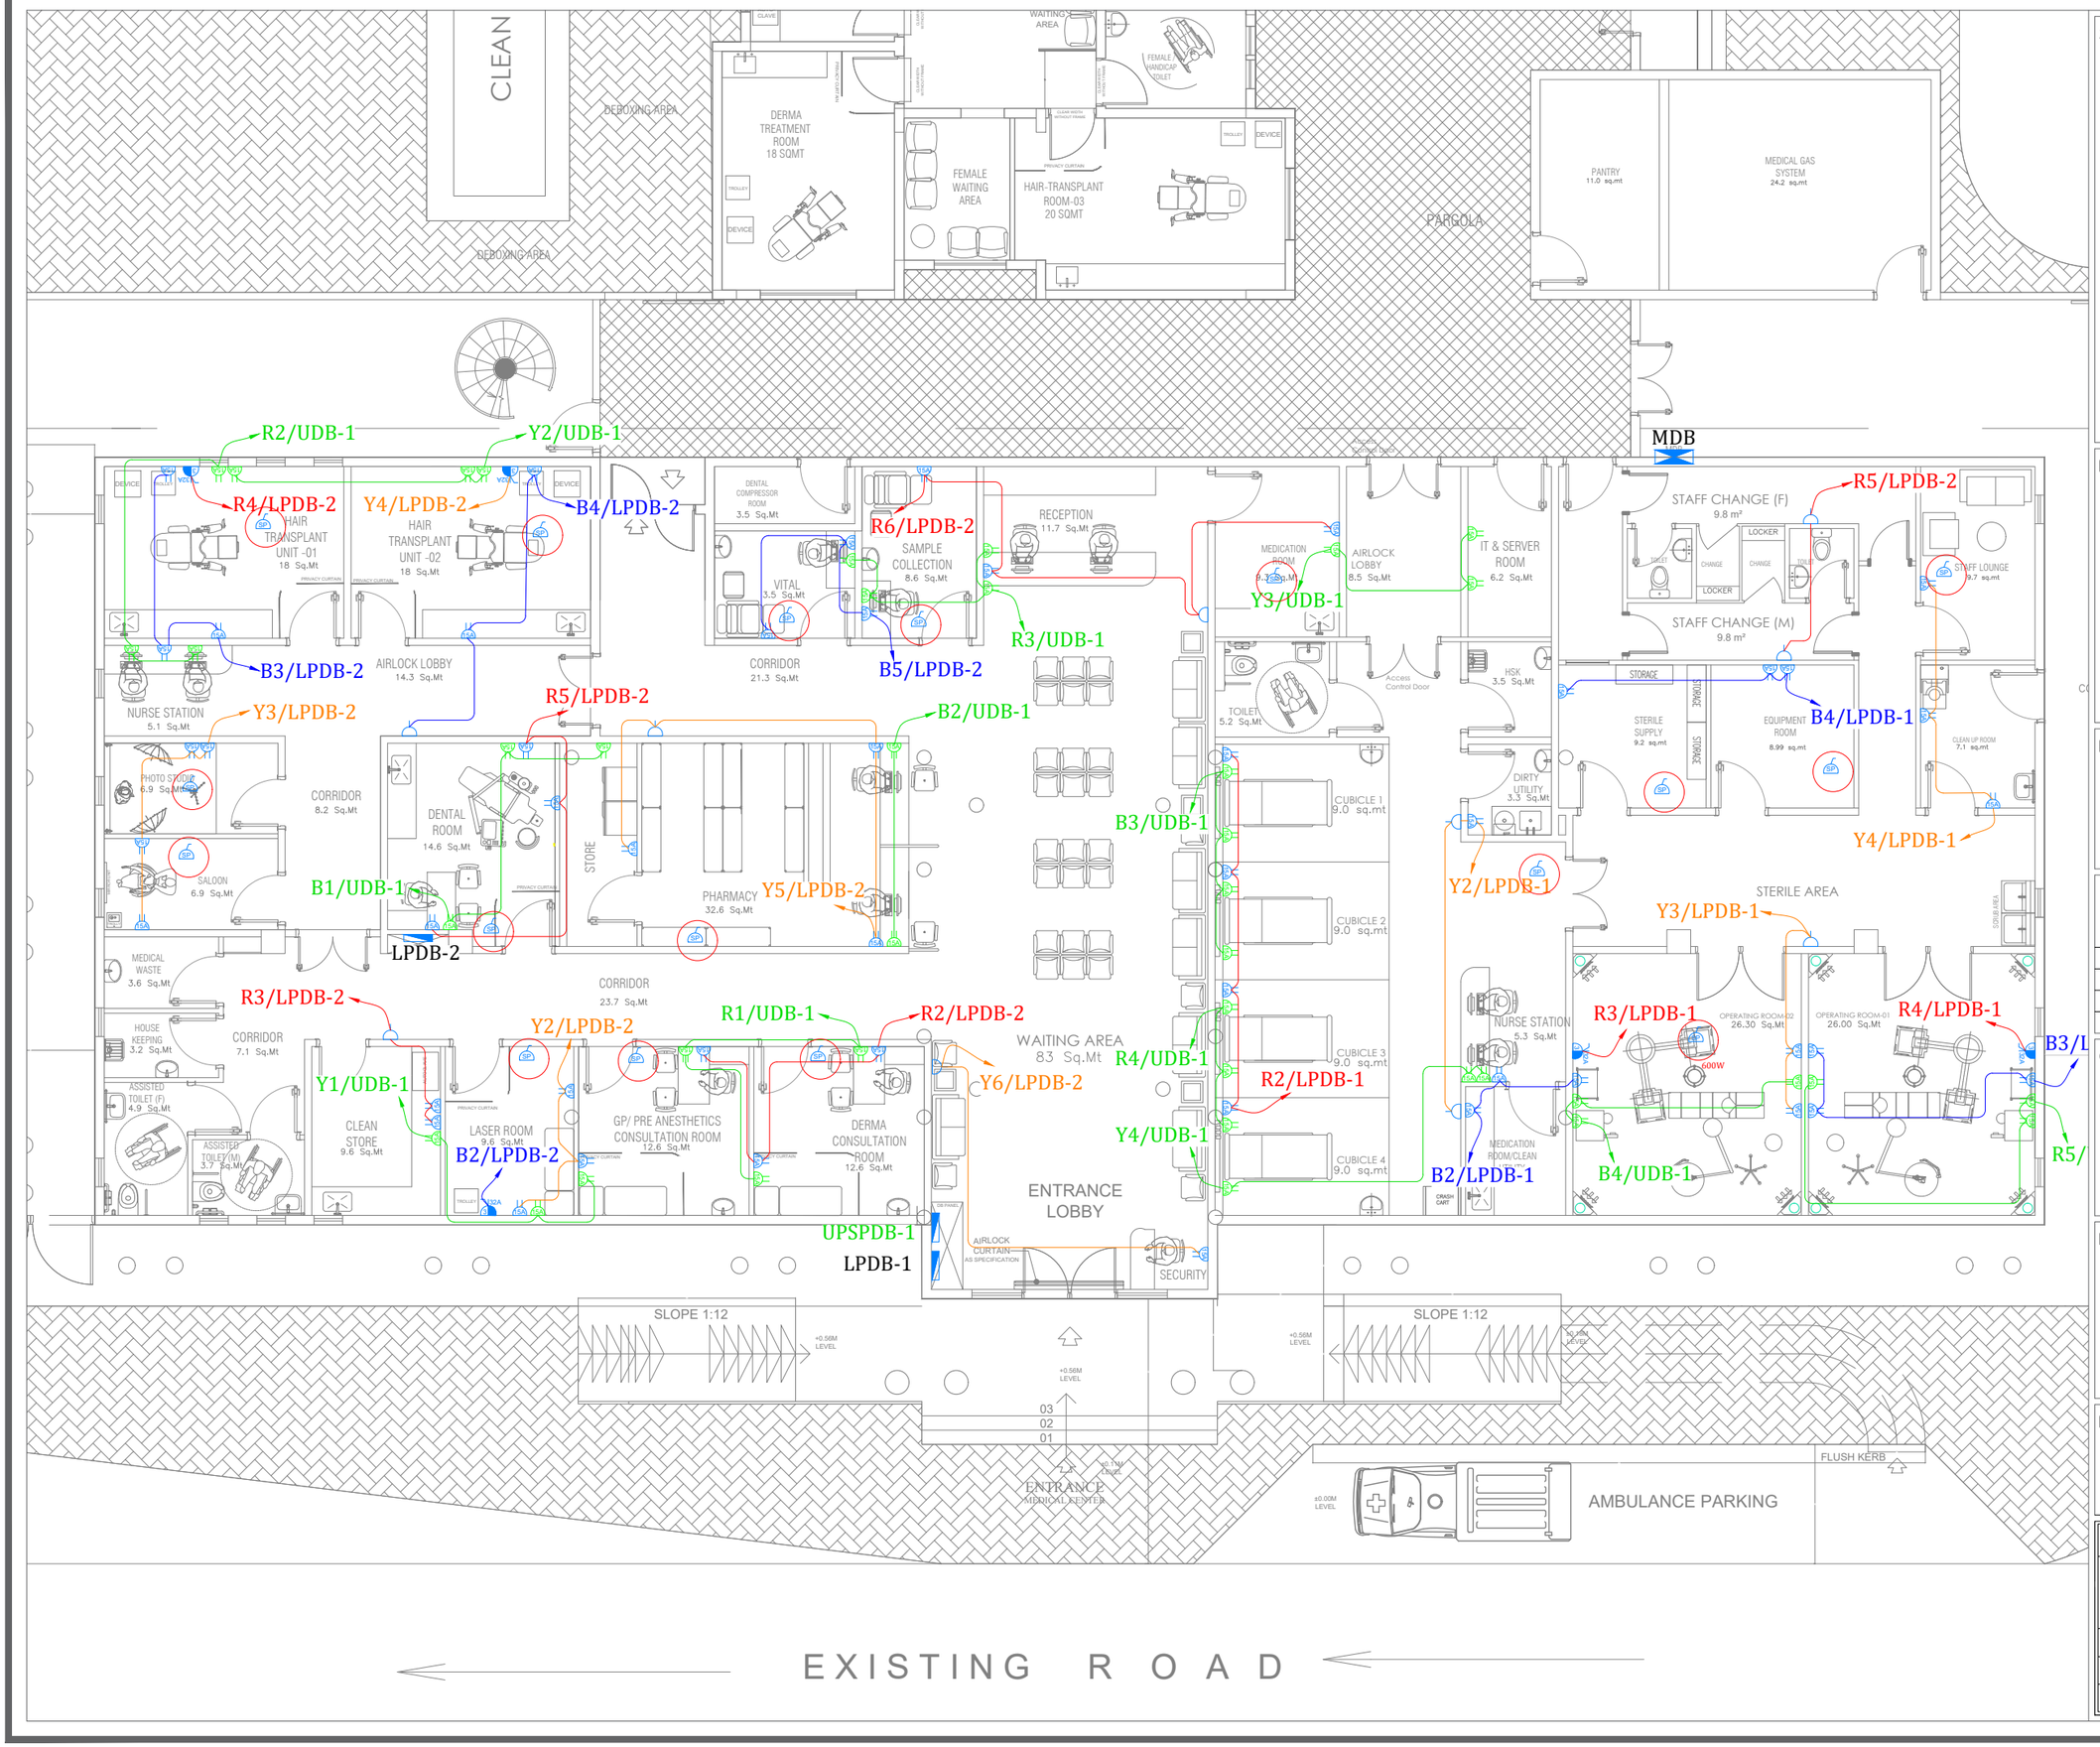

SITE PLAN :

NOTE :

PROJECT :

Multi Speciality Hospital

SR NO	DATE	DESCRIPTIONS	DRWN BY
		ISSUED FOR APPROVAL	

CLIENT :

MAIN CONTRACTOR :

MEP CONSULTANT:

PROJECT NO:			
DRAWING TITLE: GROUND FLOOR - ELECTRICAL- POWER LOAD			
DRAWING NO :			DATE:
DRAWN BY:	CHECKED BY:		SCALE:
SERIAL NO:	SHEET NO:		REV.NO: